





PLANTA BAJA


Espacio circulatorio (PAV) A.C.: 5.00 m

Desagüe vehicular tipo guardaganado

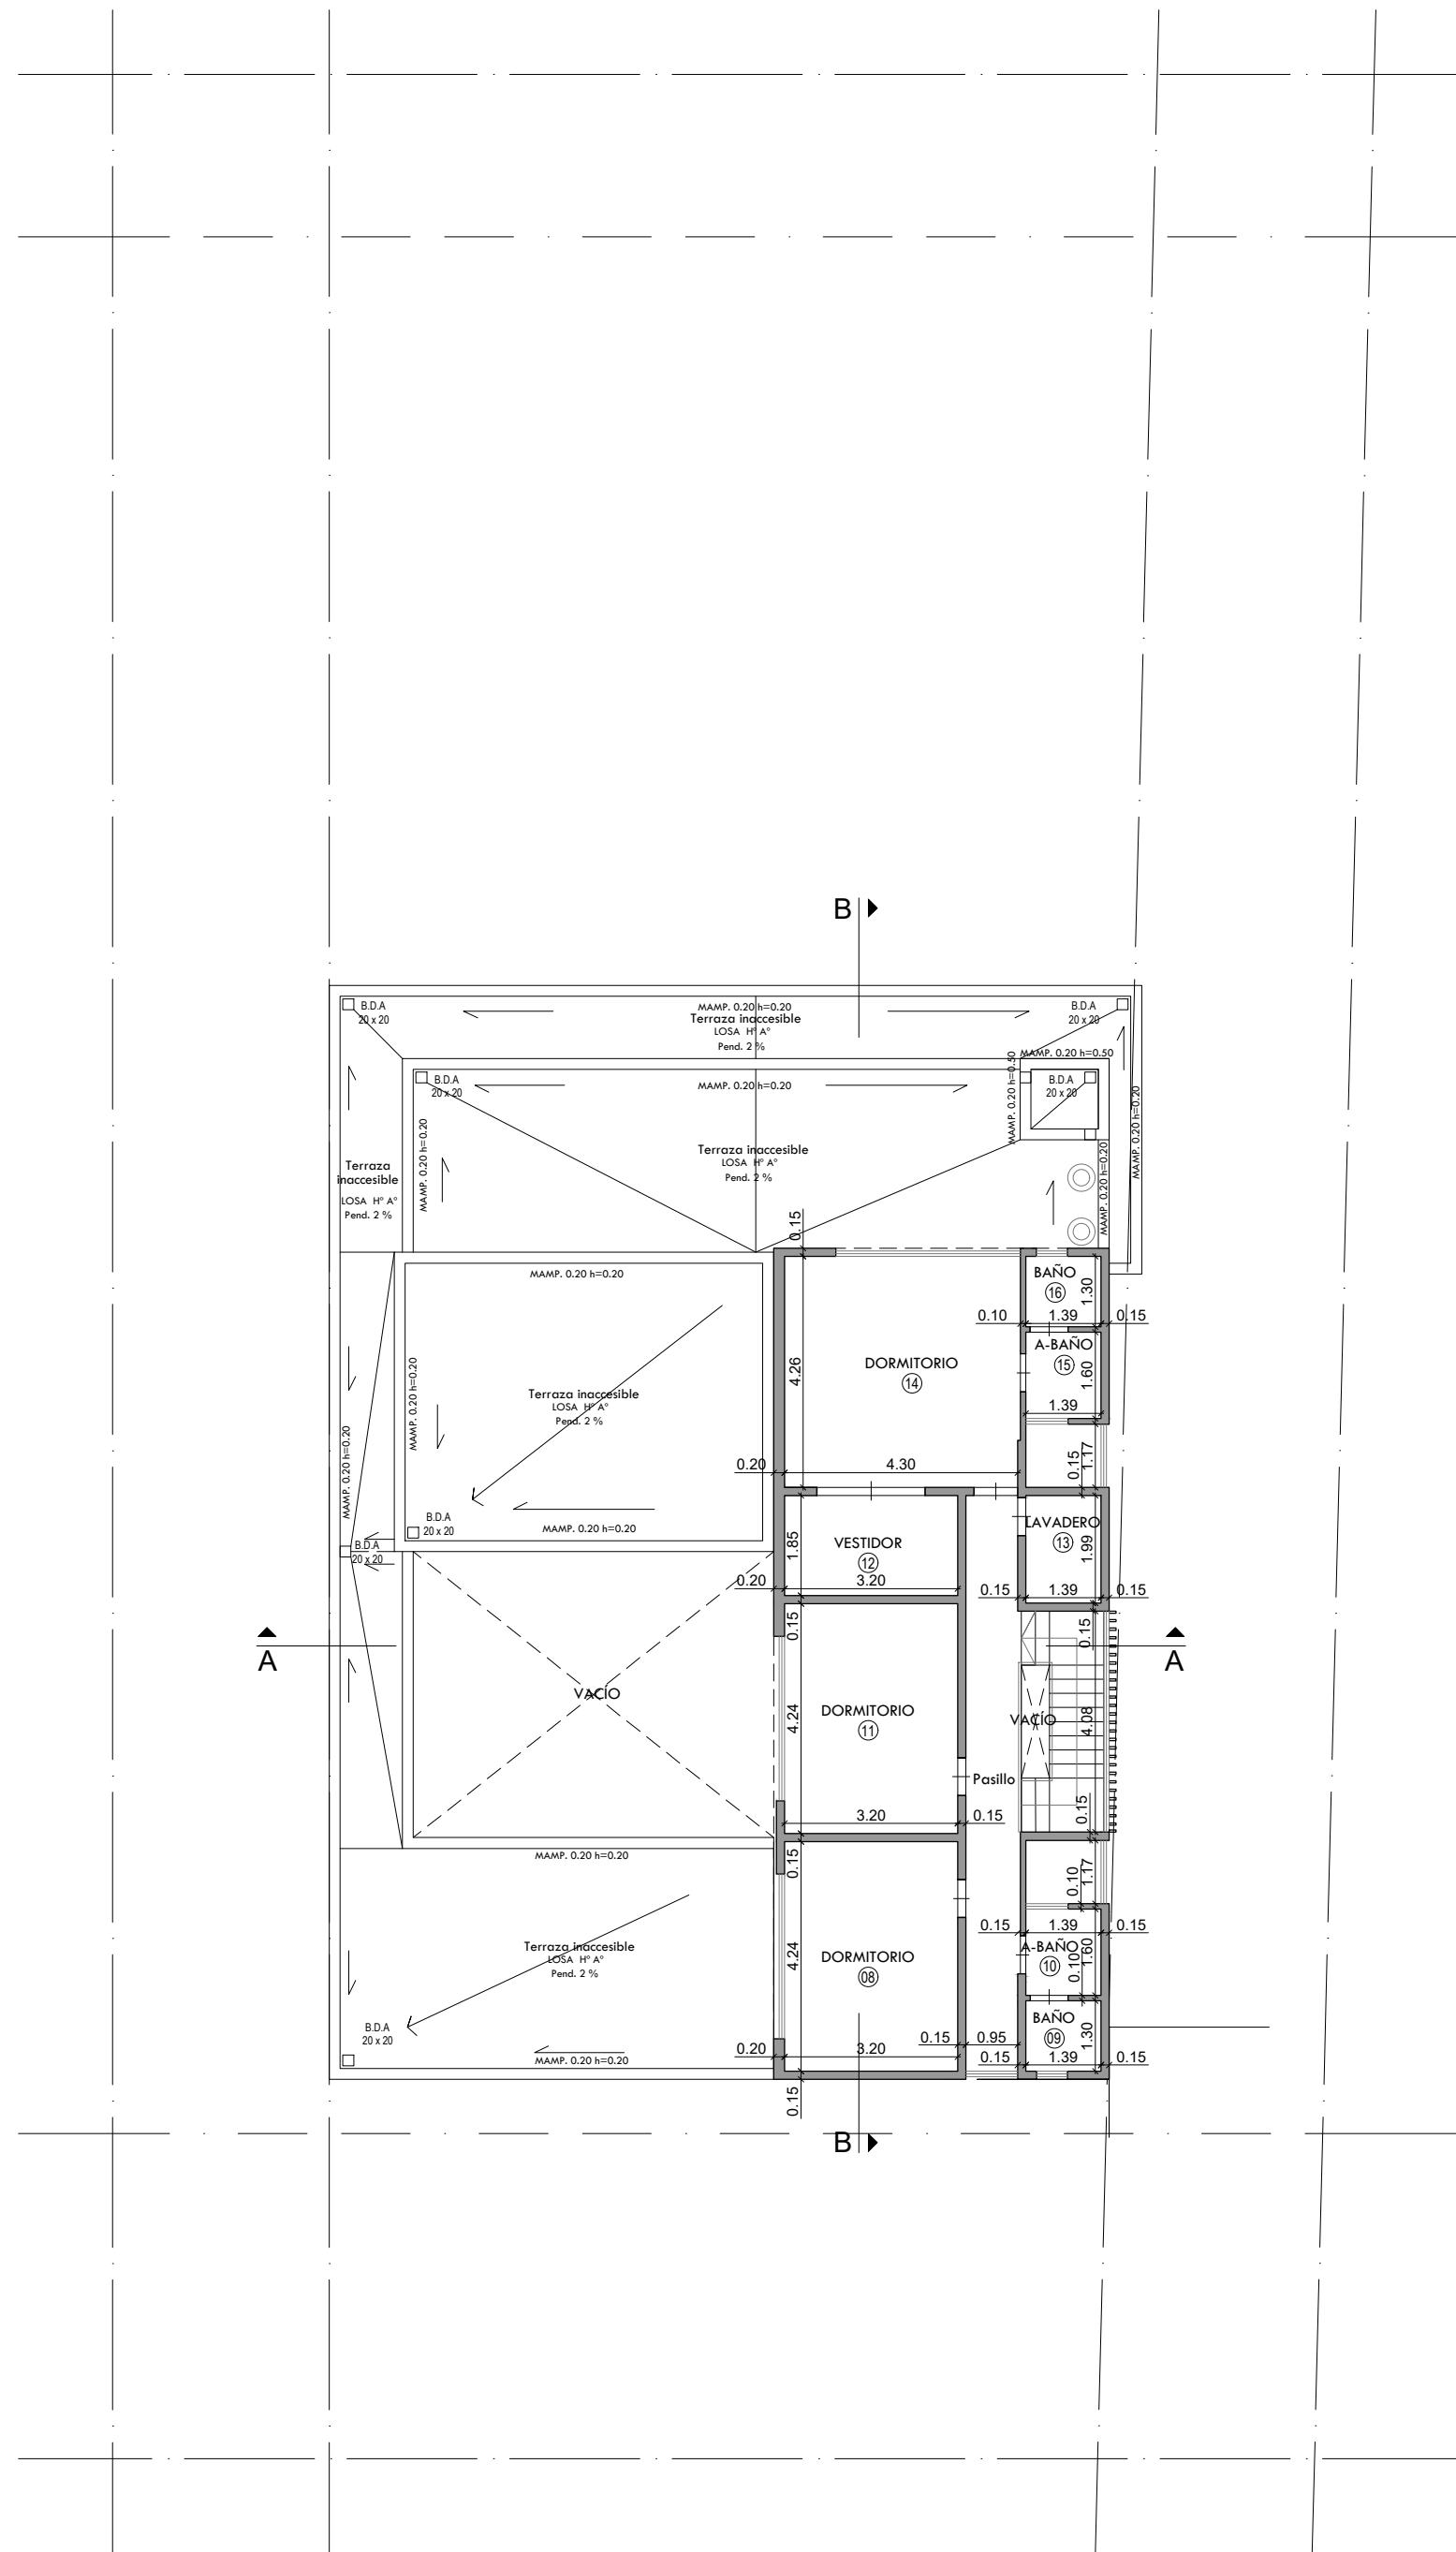


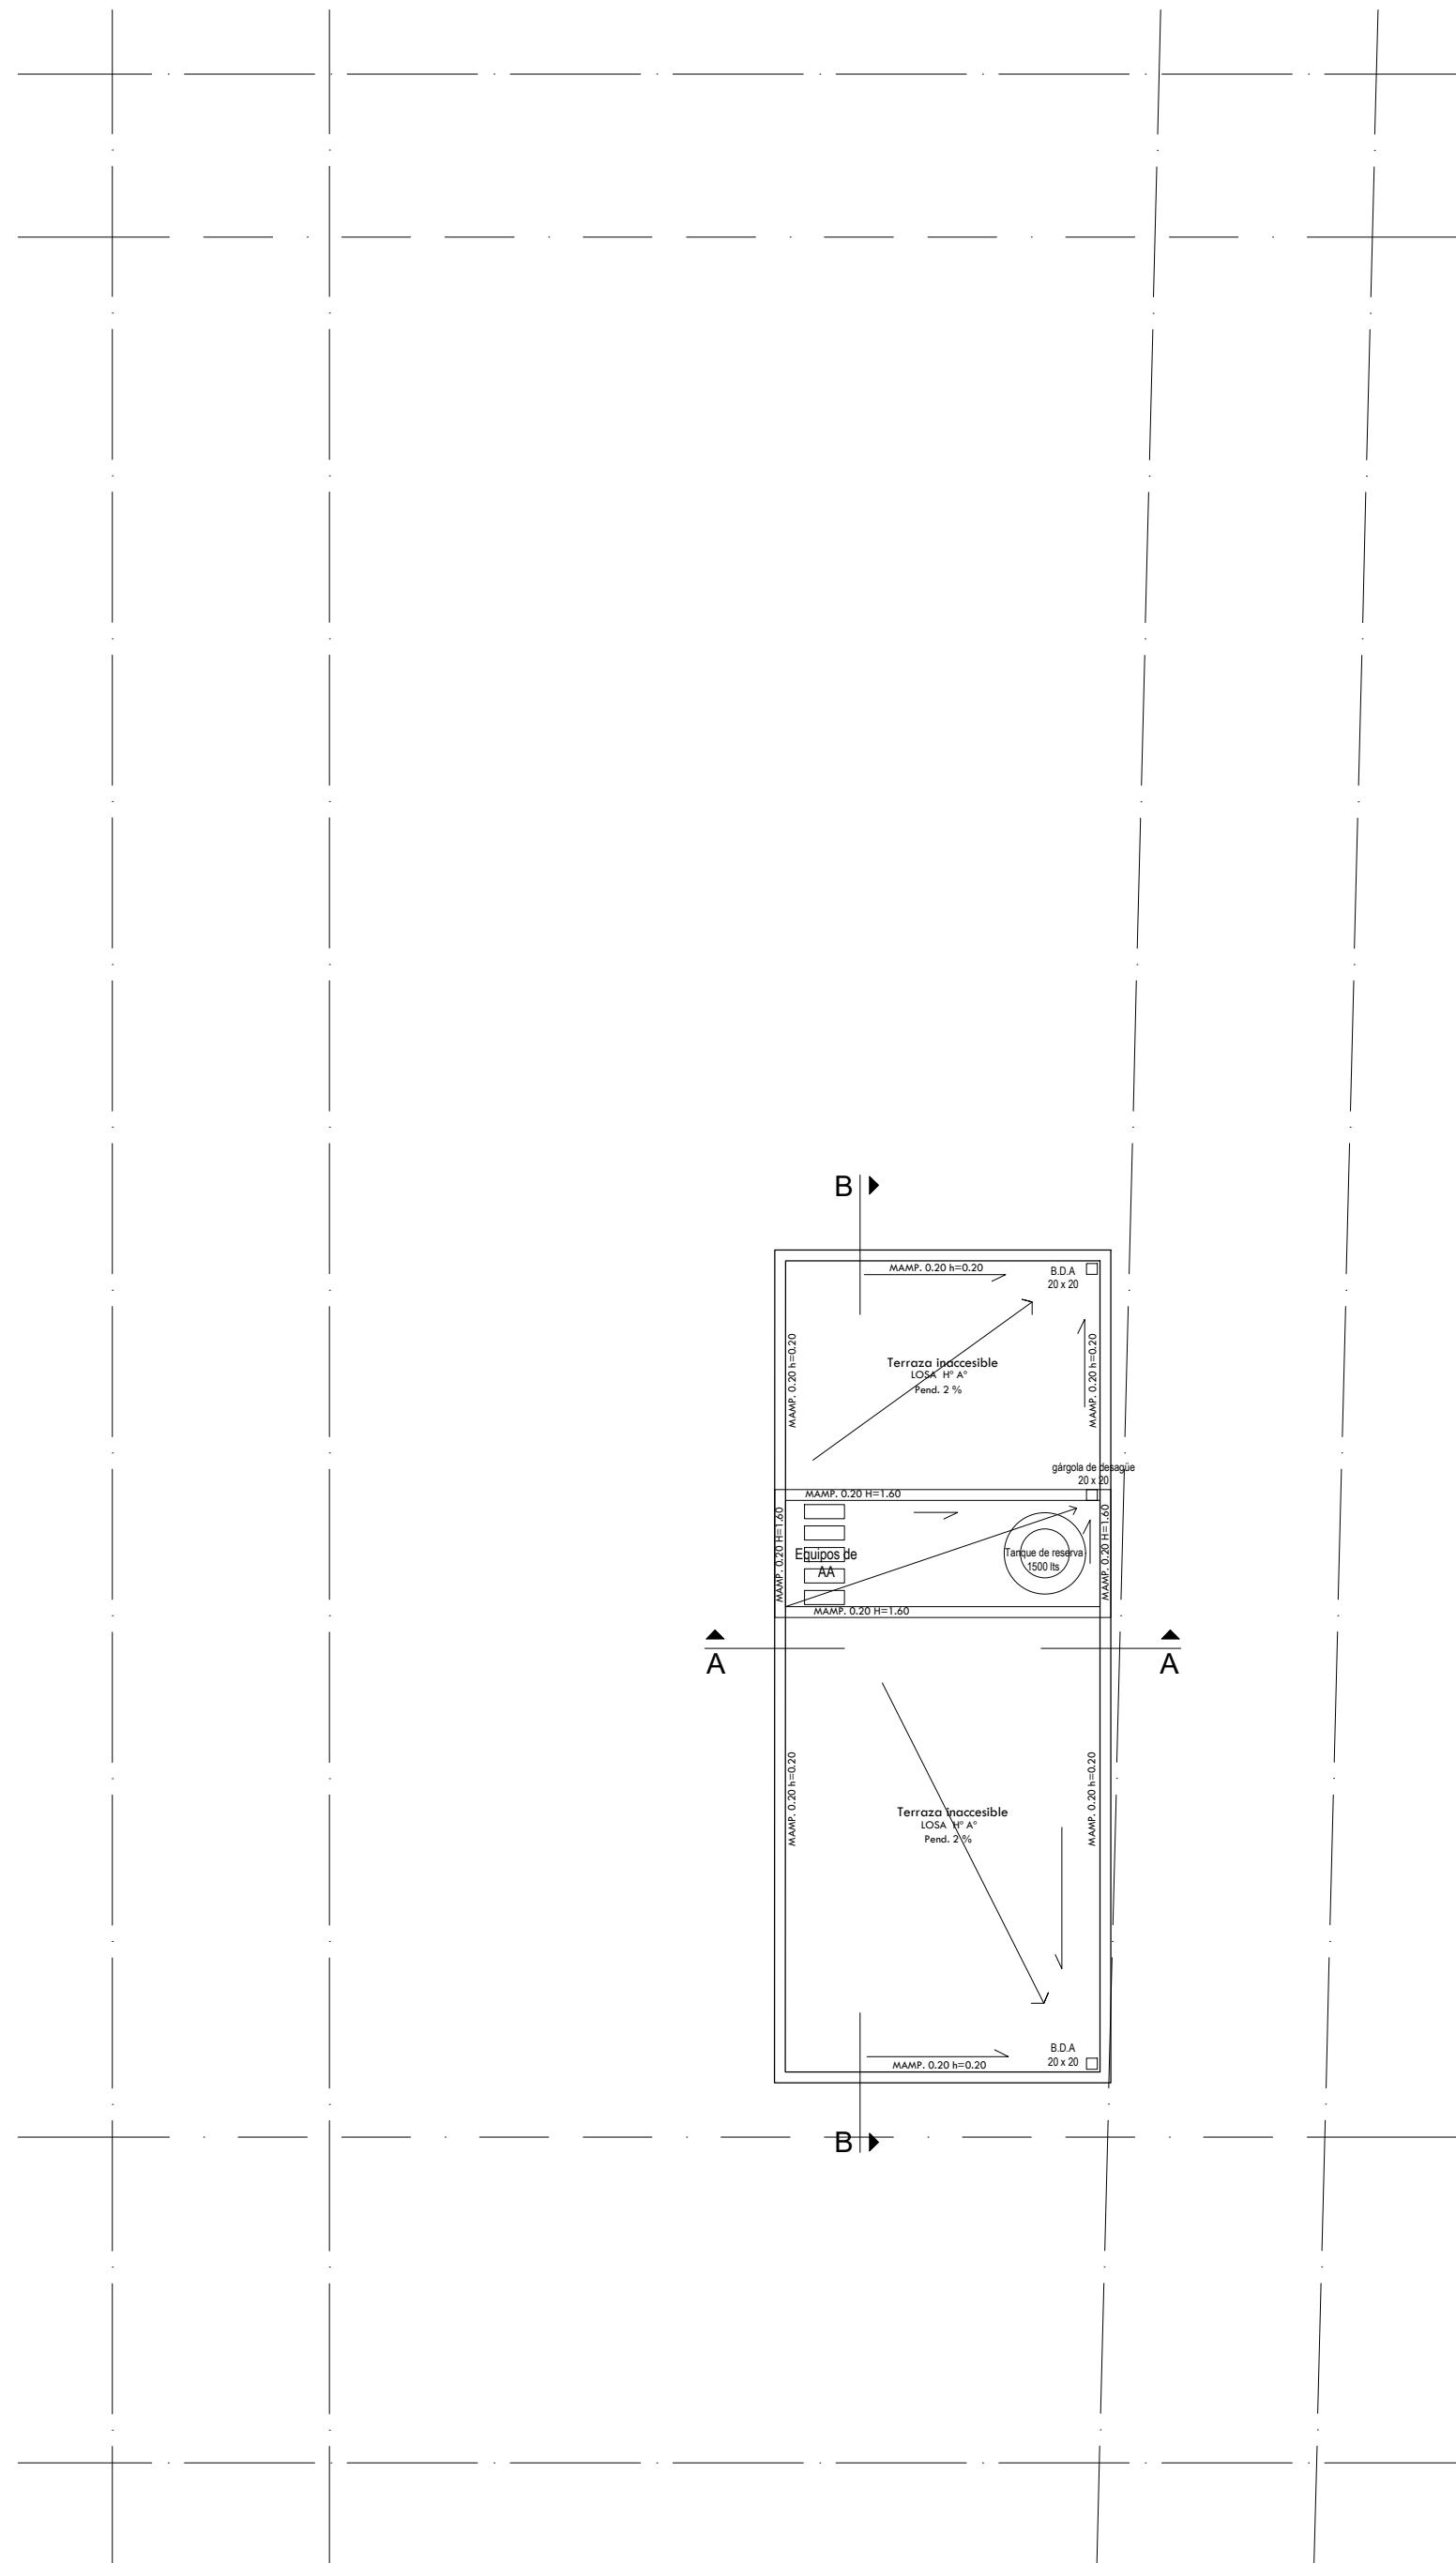

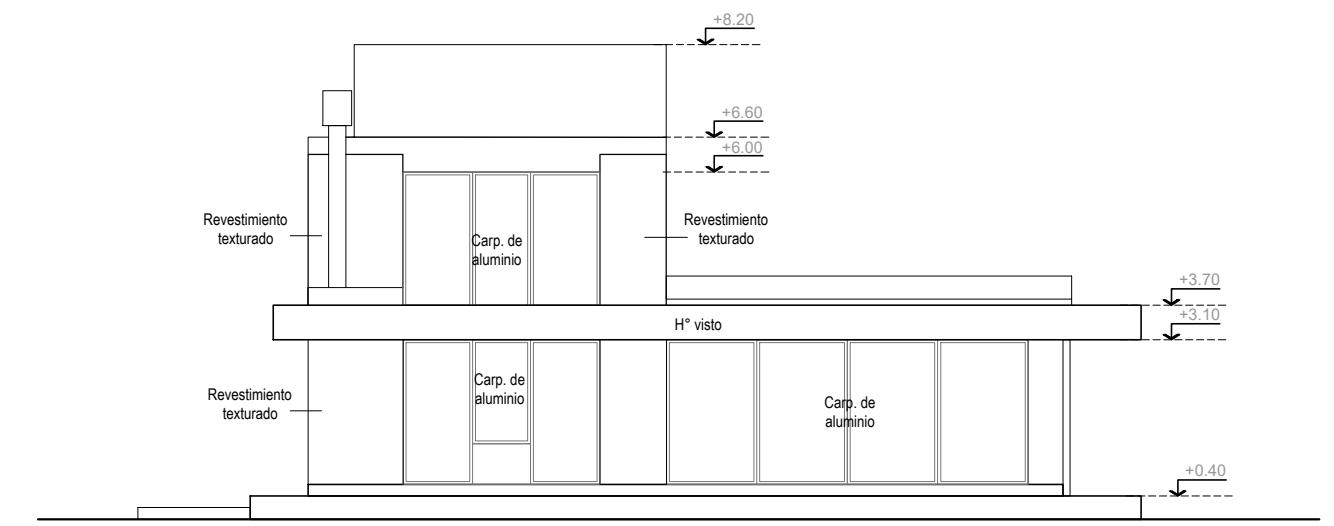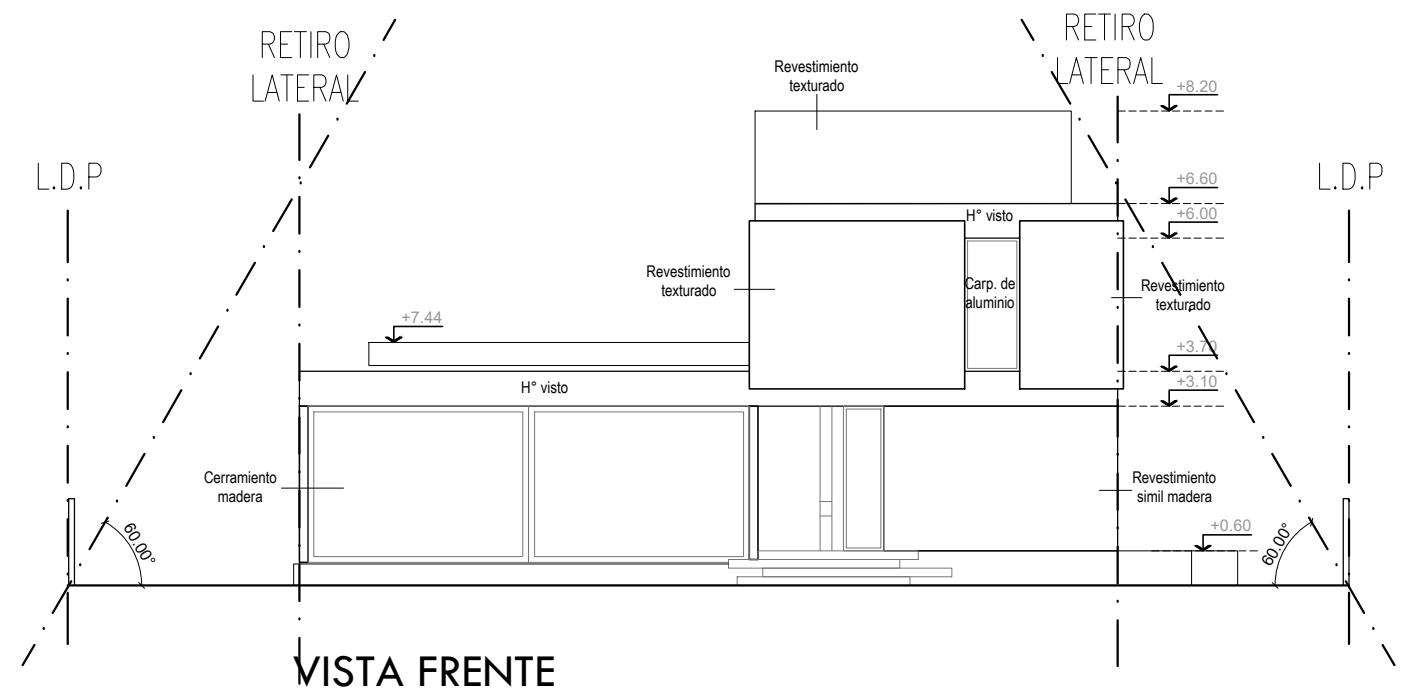


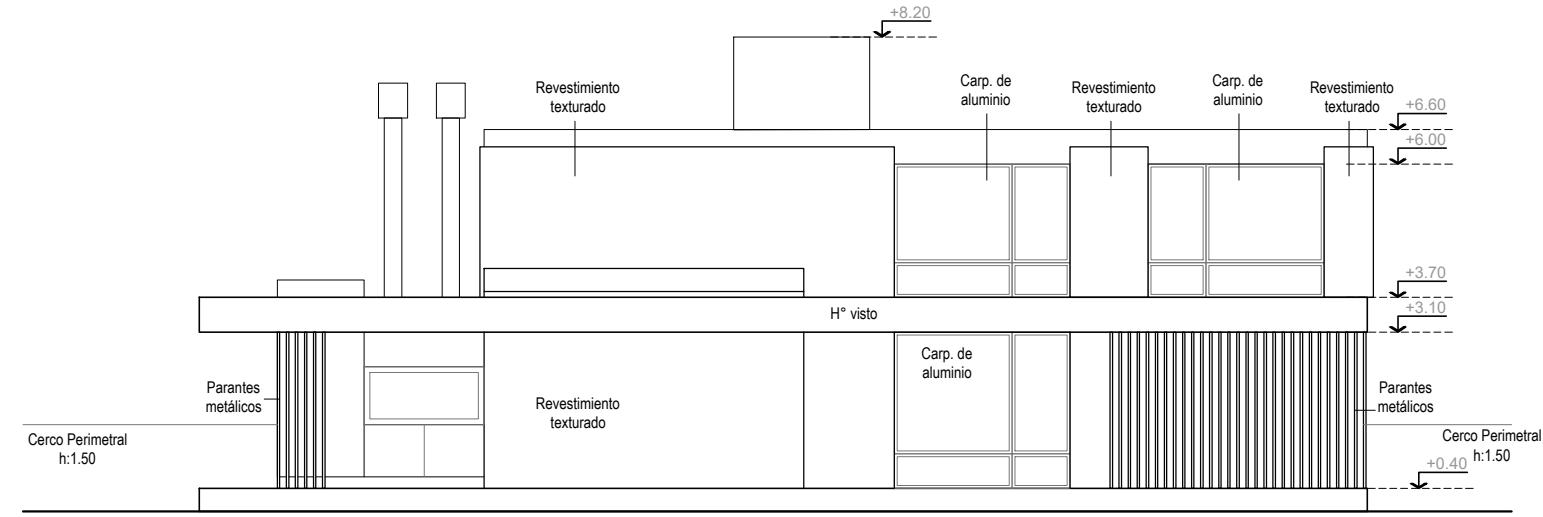


VISTA LATERAL IZQUIERDA

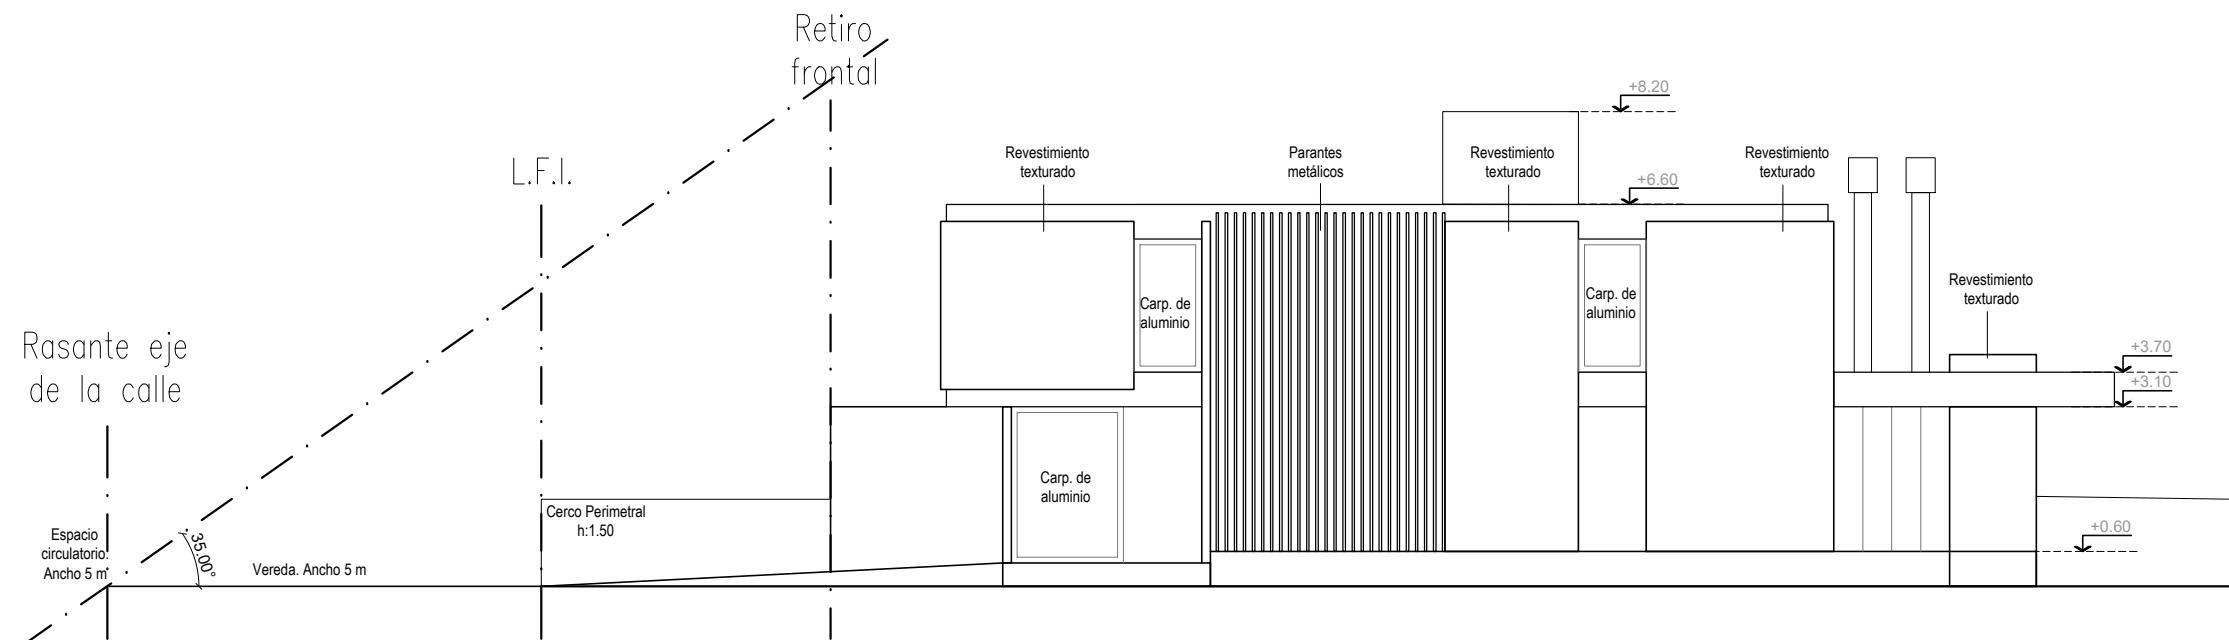


VISTA LATERAL DERECHA

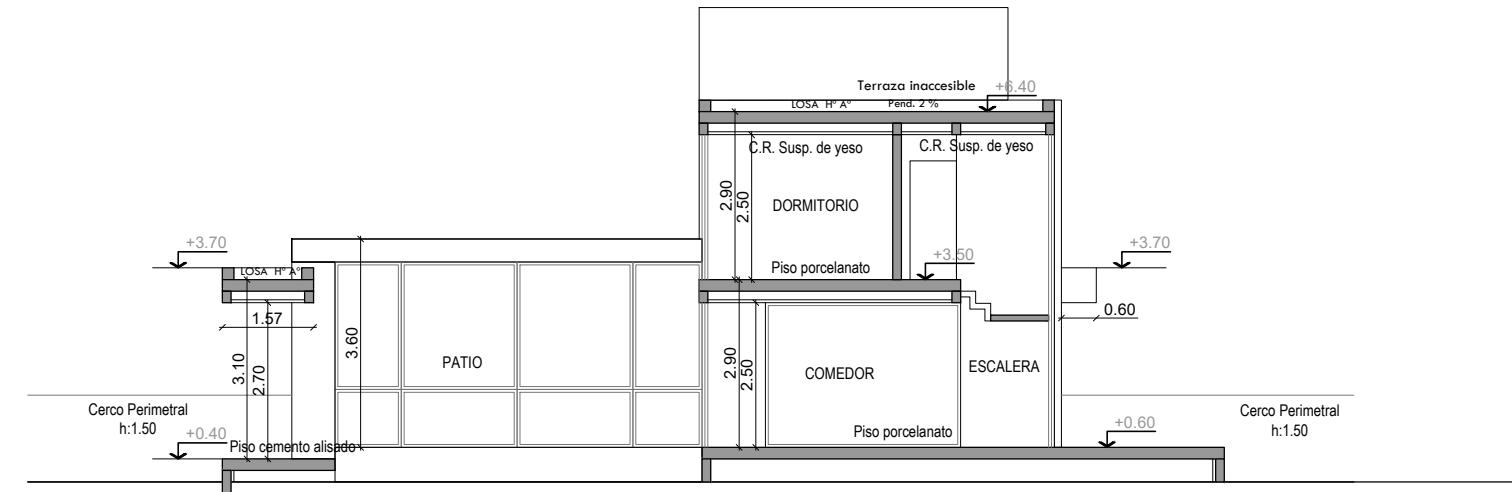


CORTE A-A

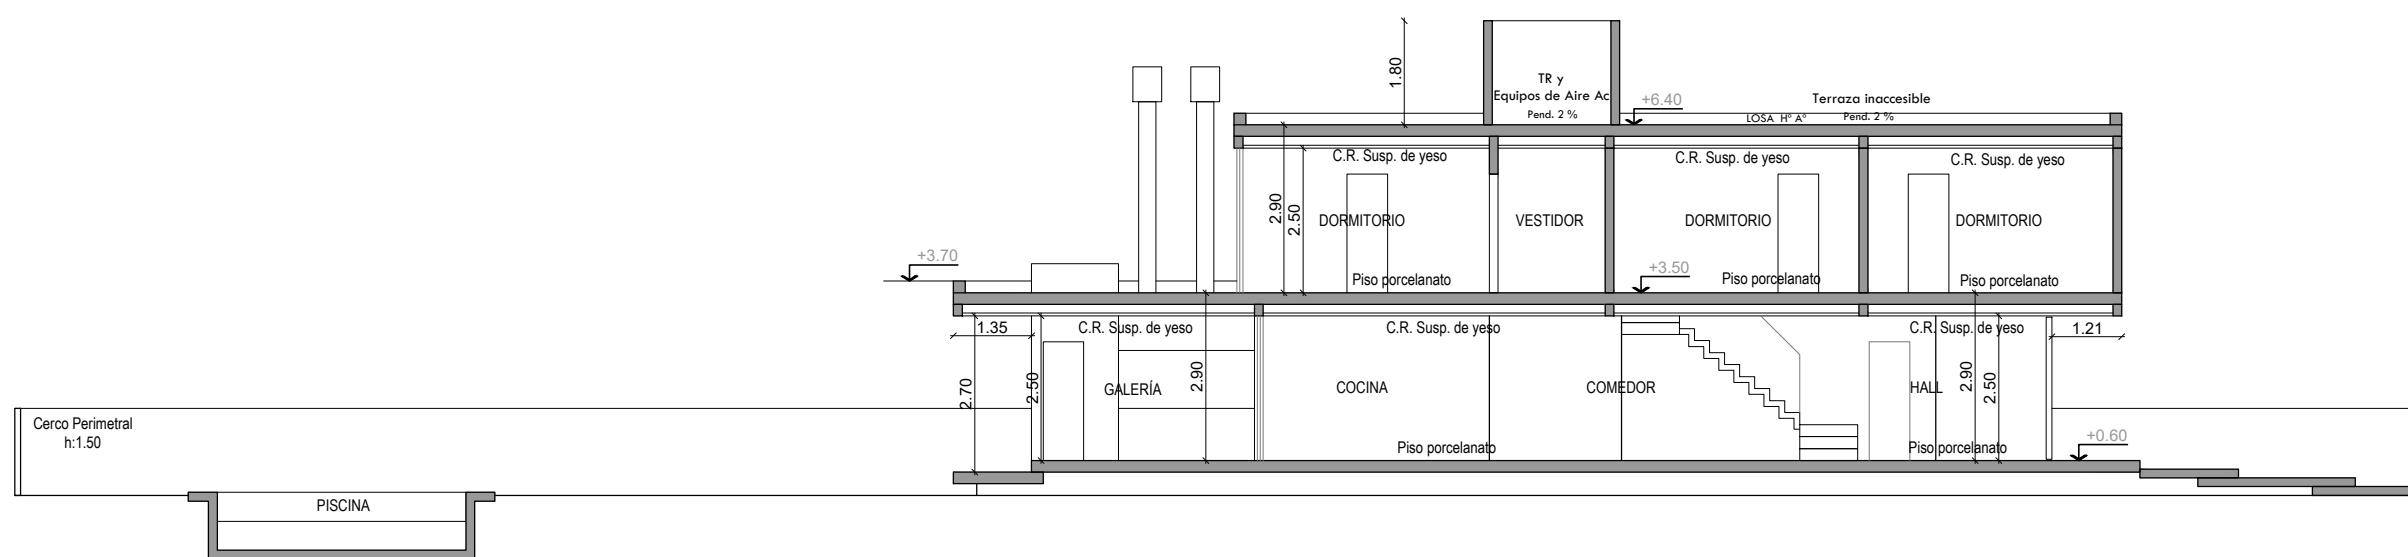


CORTE B-B

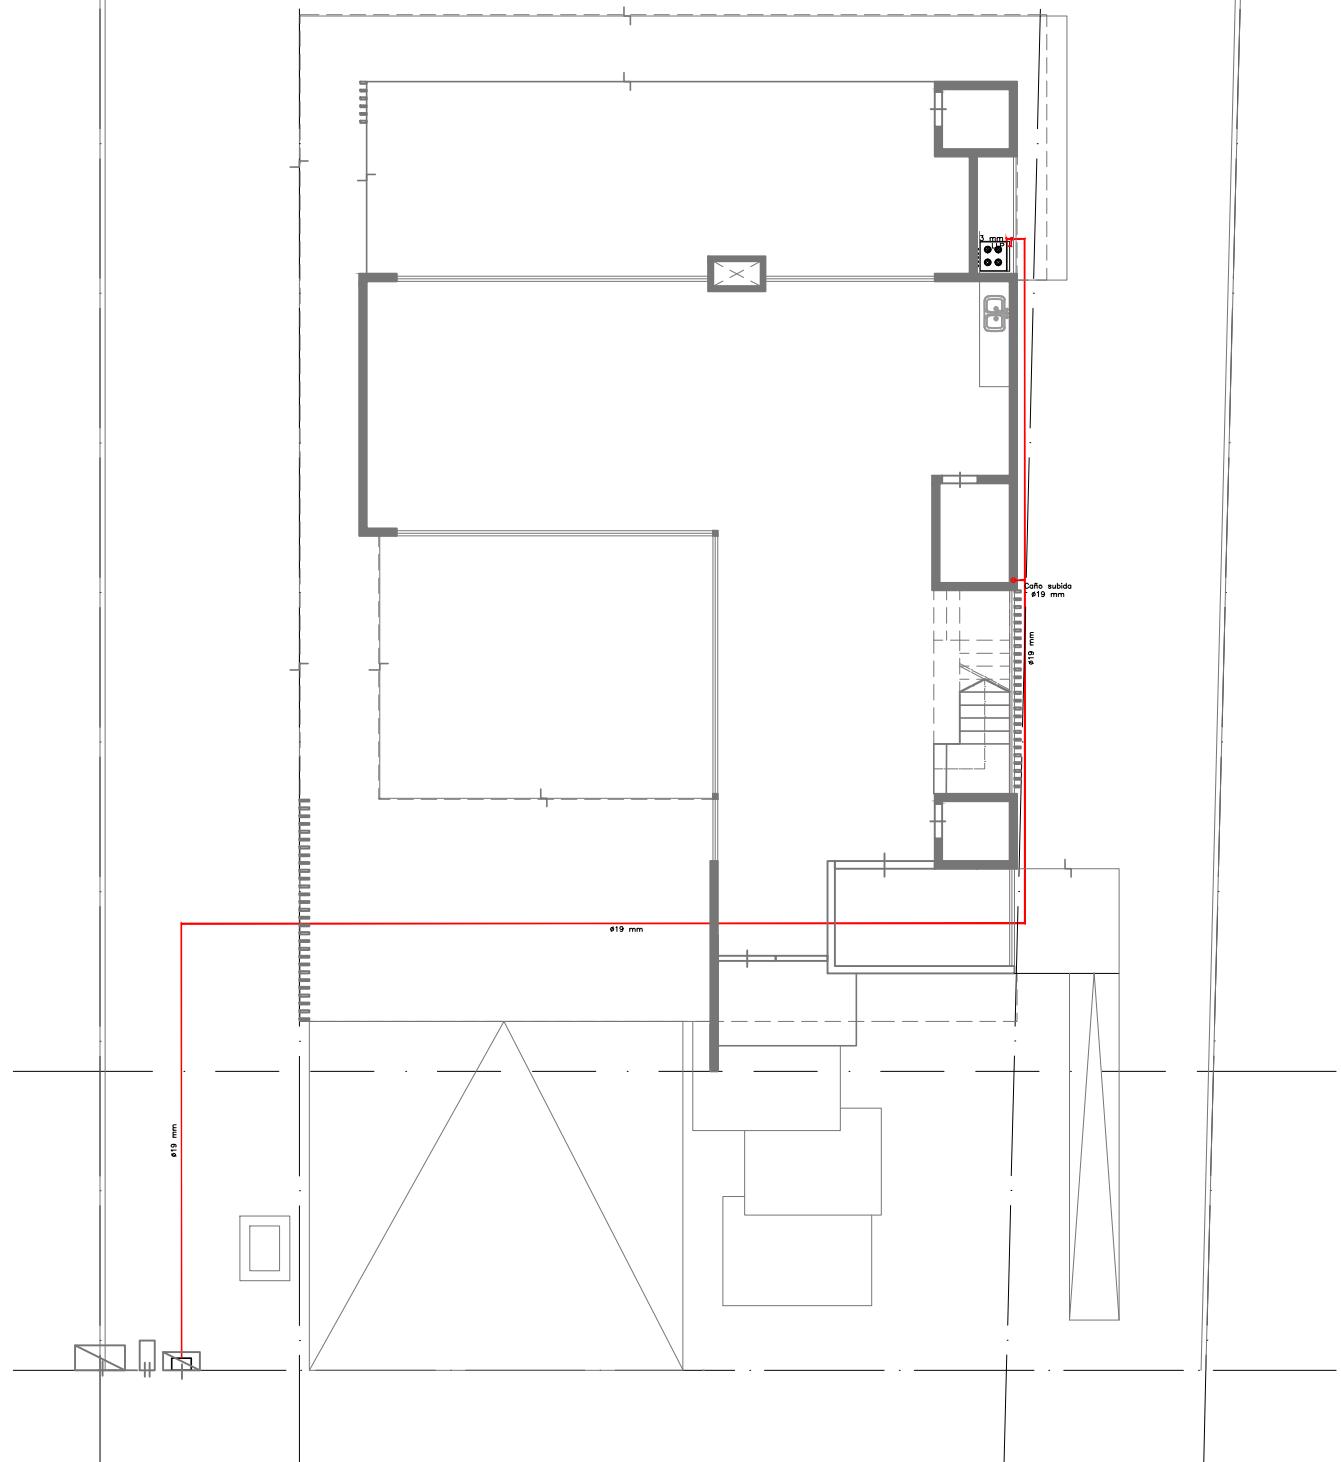


PLANTA BAJA

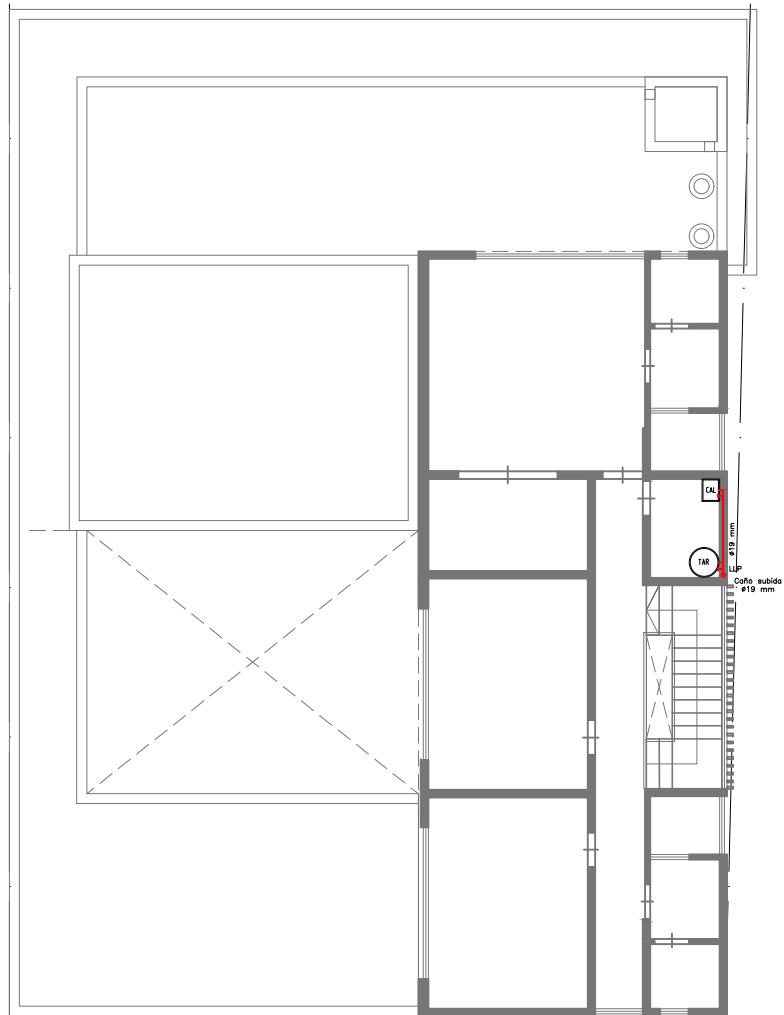


PLANTA ALTA

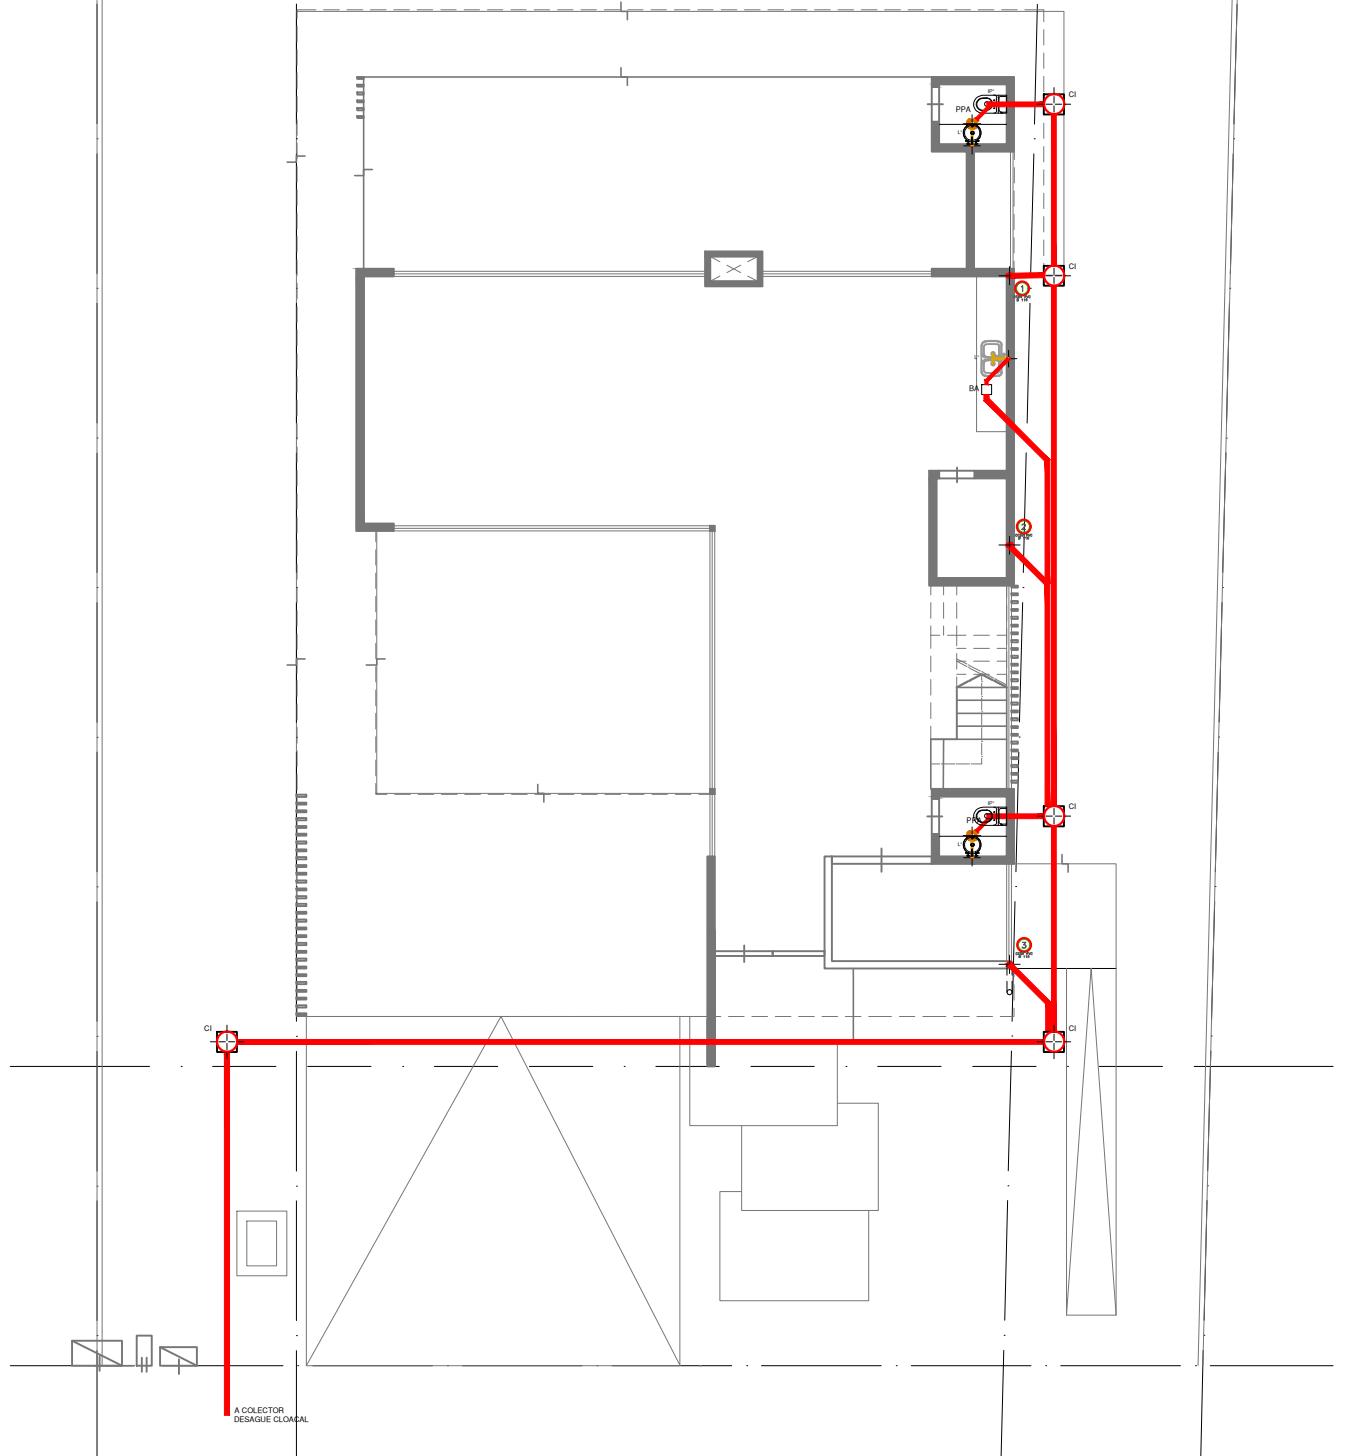


PLANTA BAJA

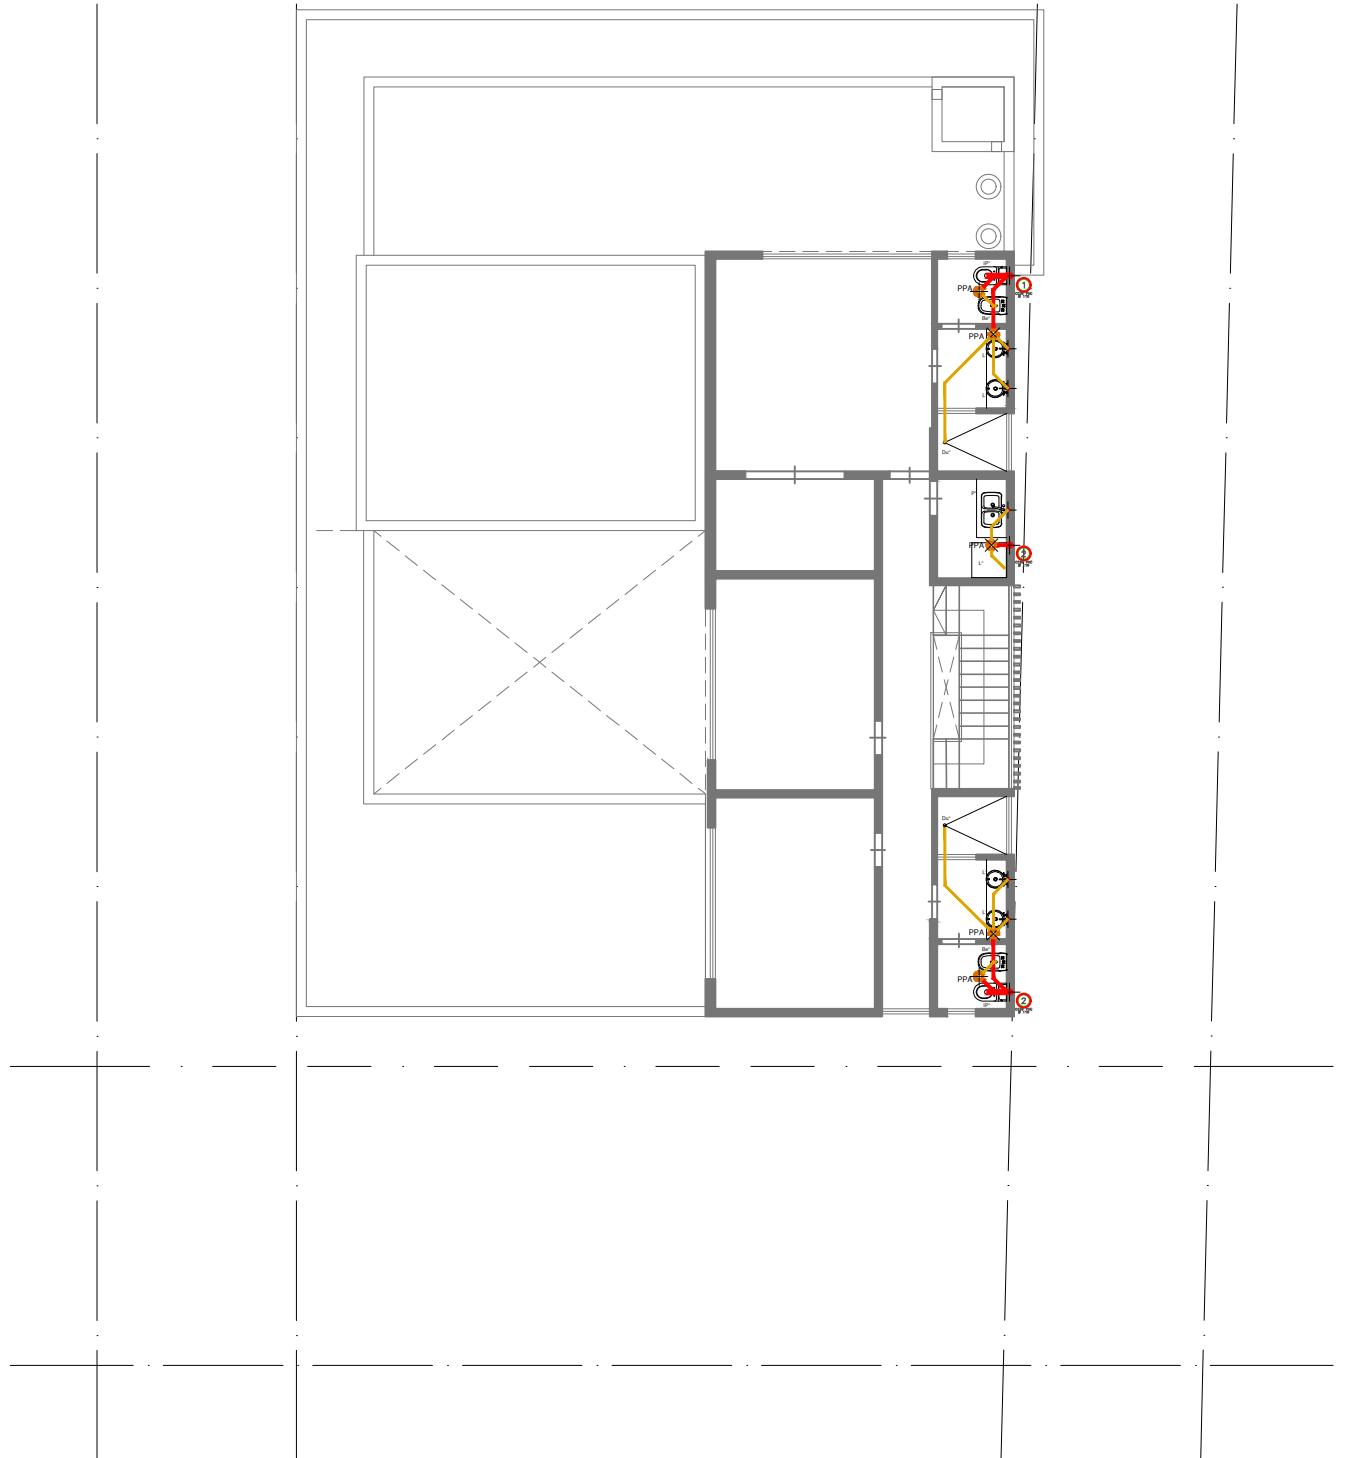


PLANTA ALTA

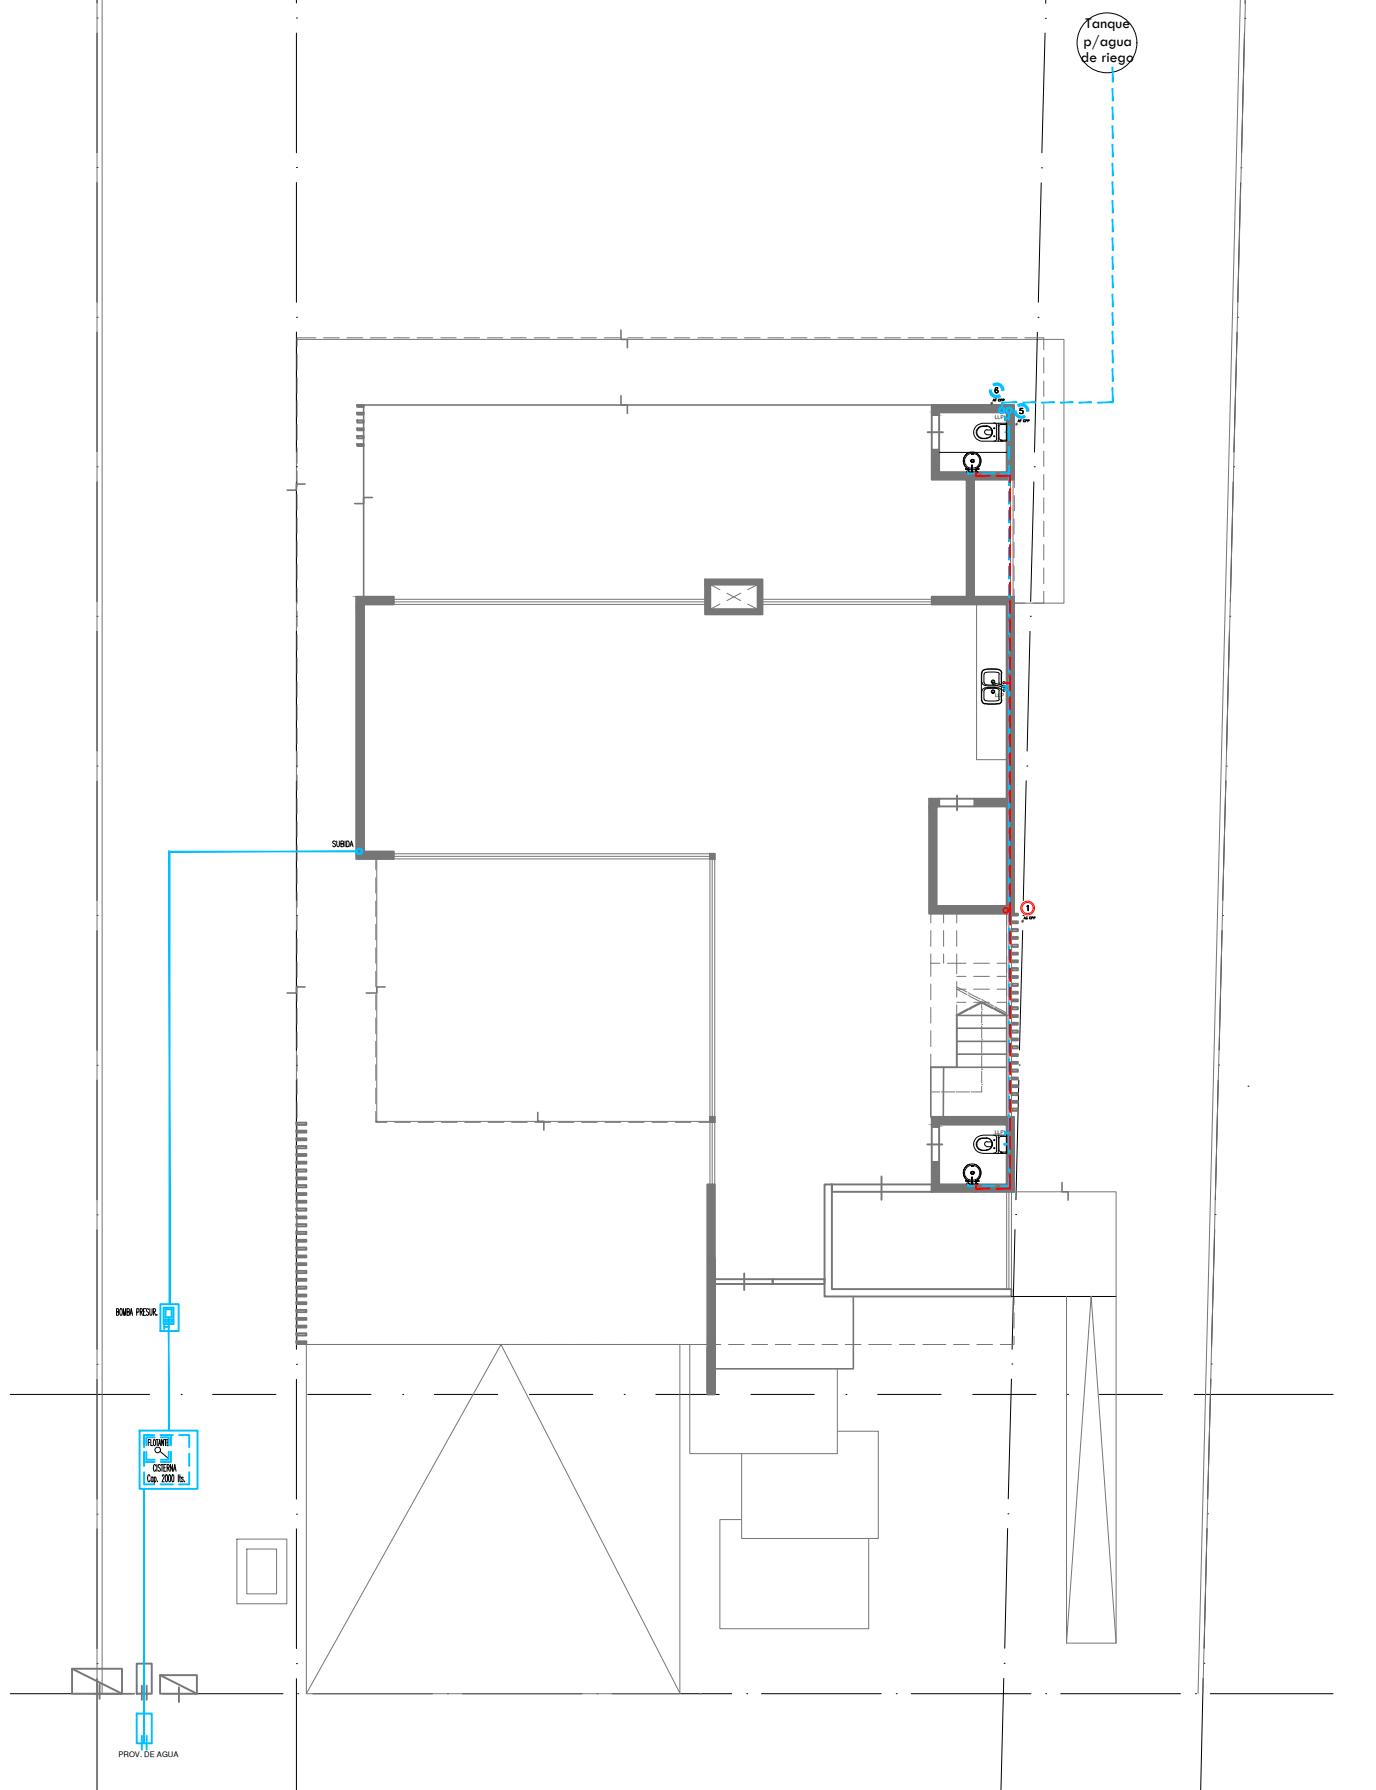


PLANTA BAJA

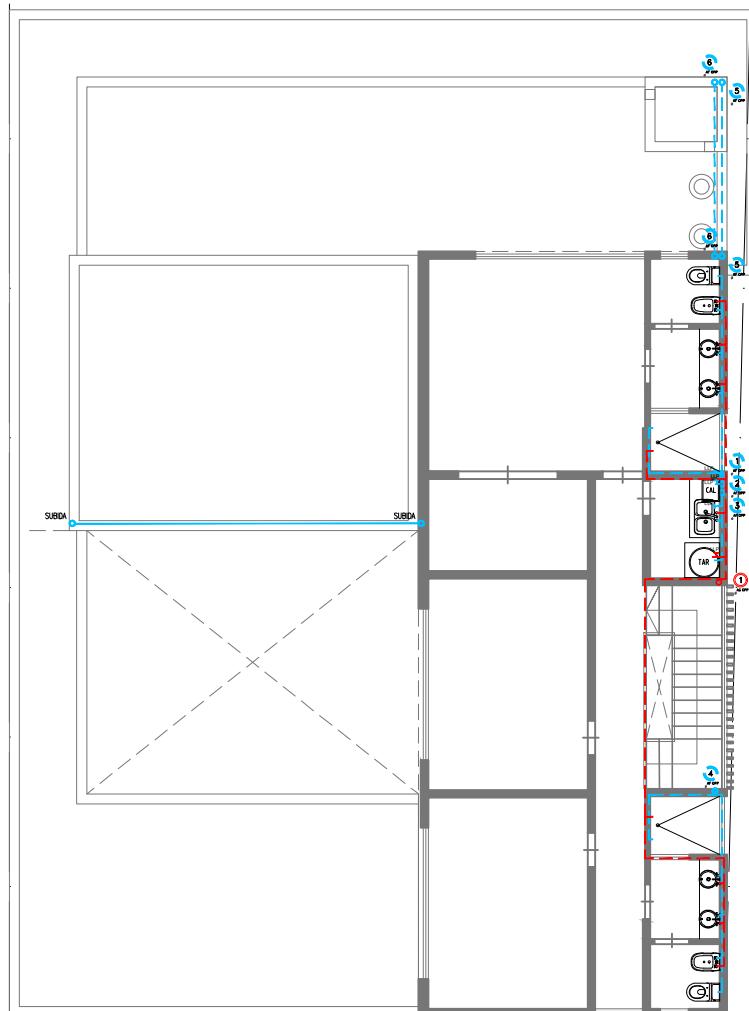


PLANTA ALTA

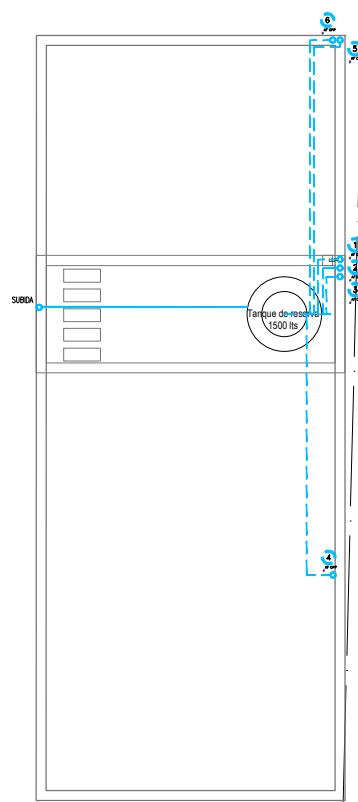


PLANTA DE TECHOS

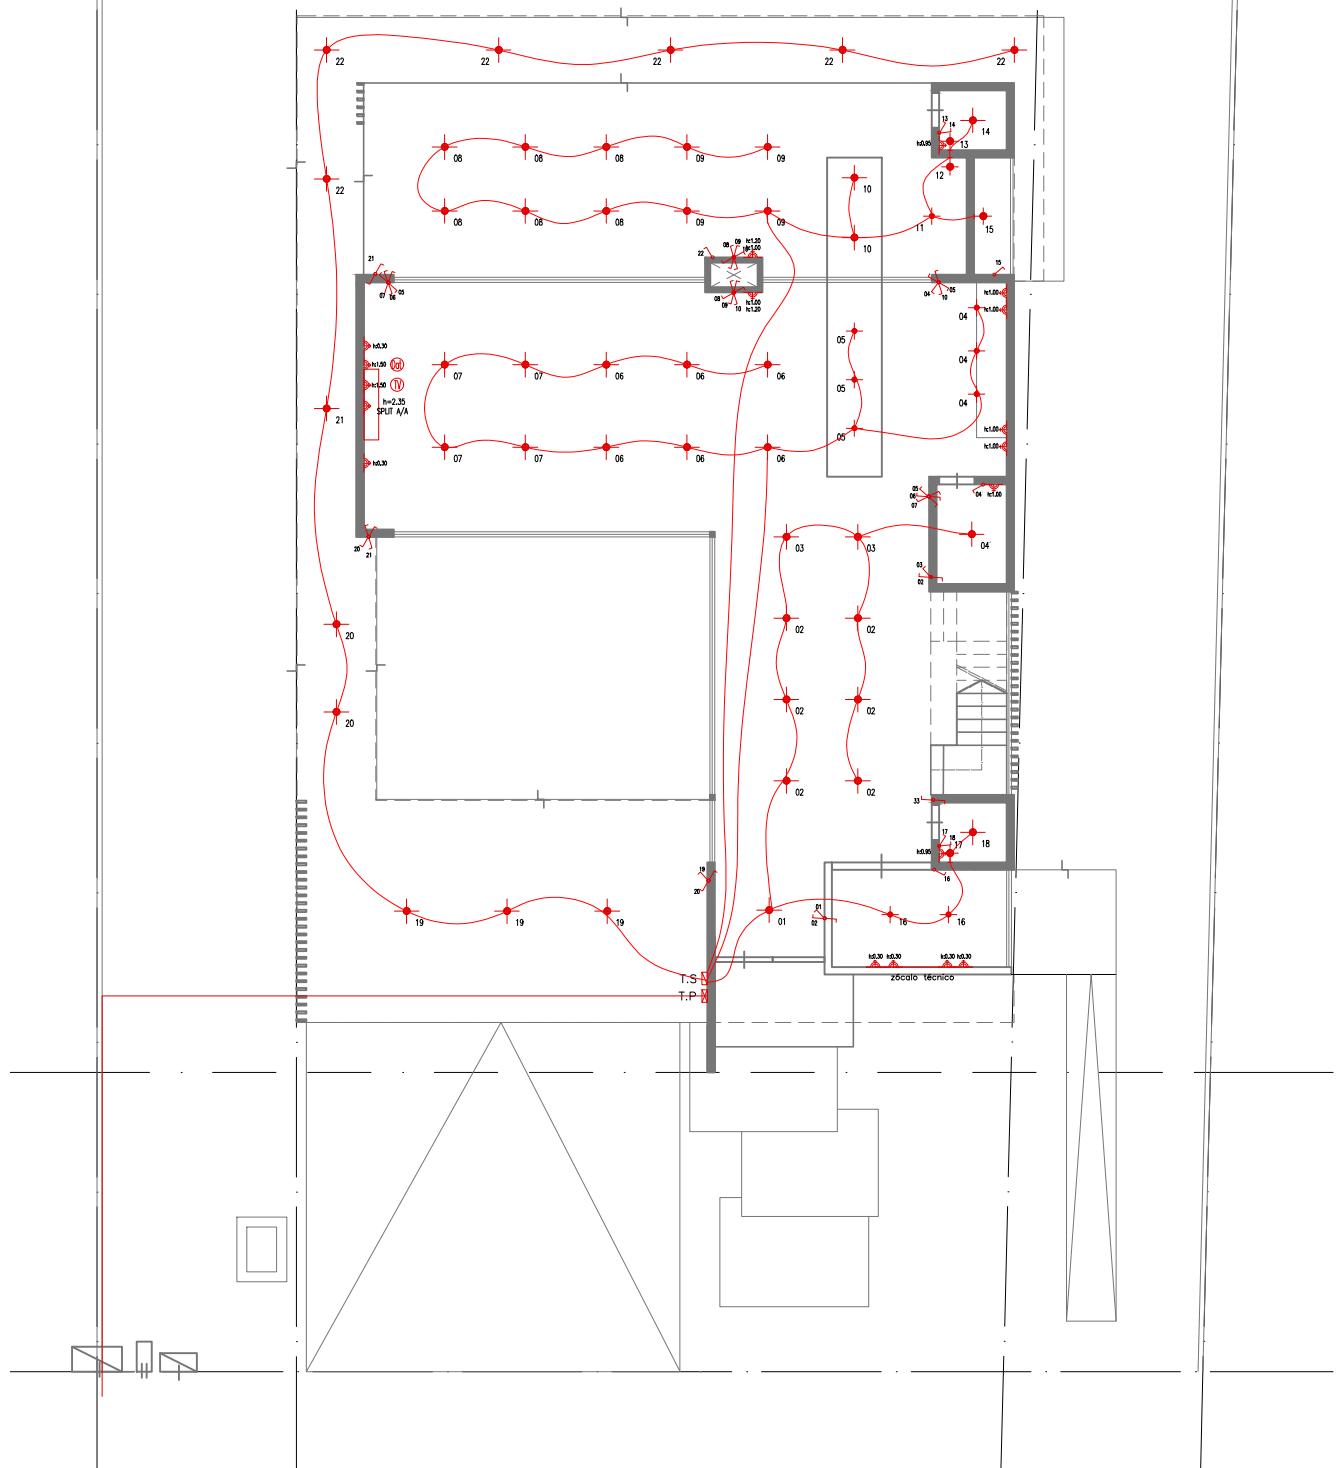


PLANTA BAJA

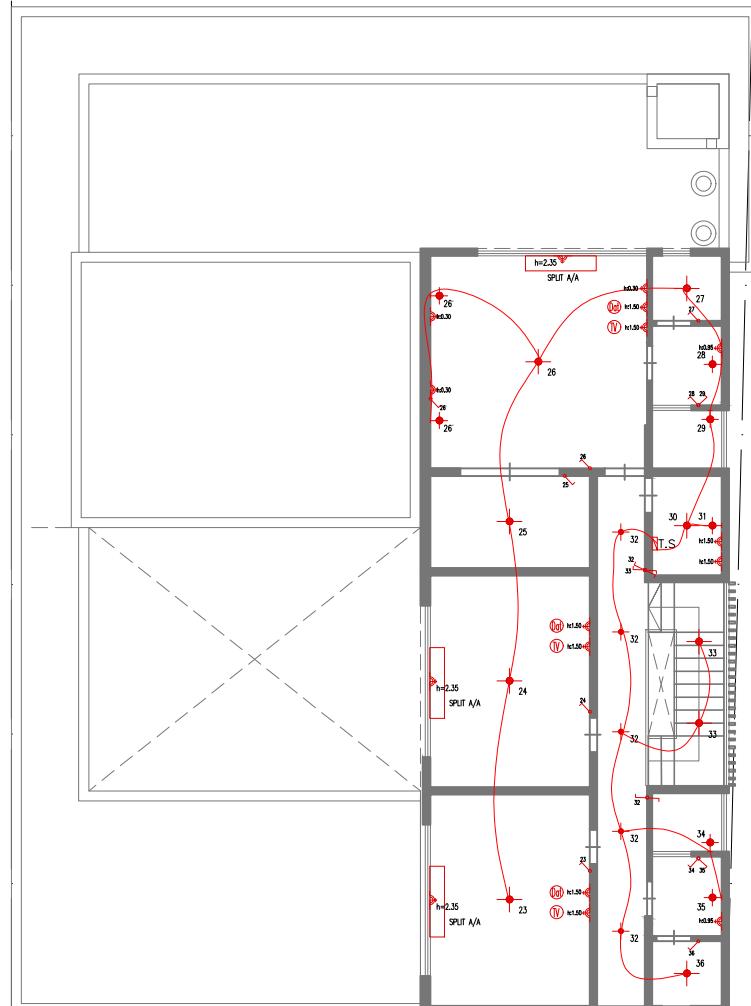


PLANTA ALTA

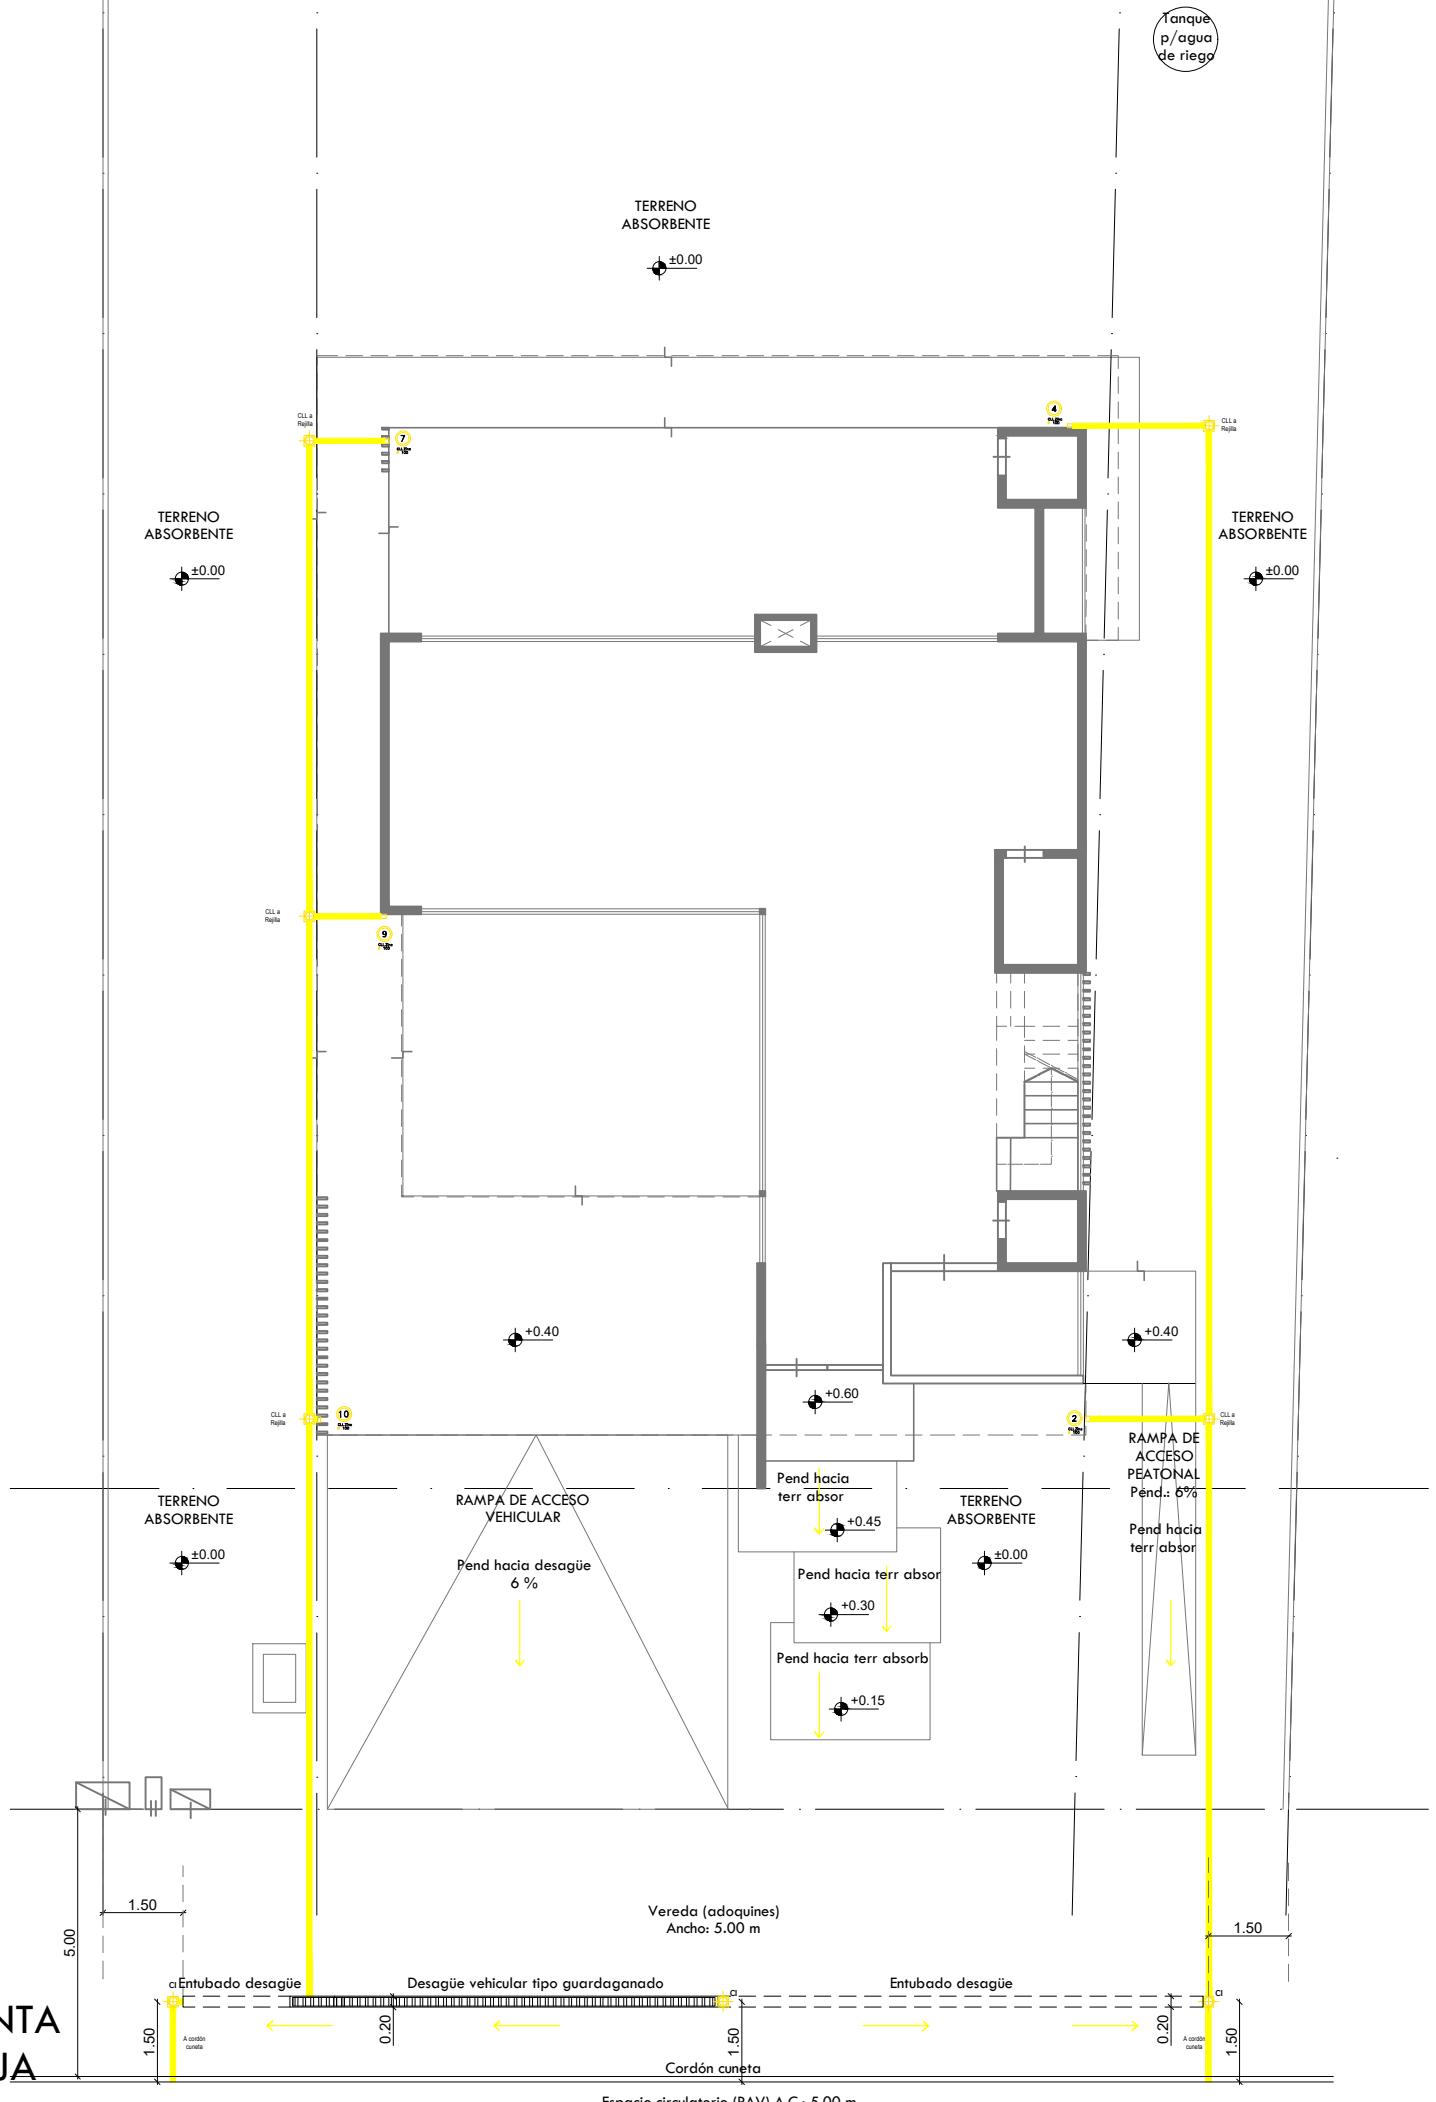


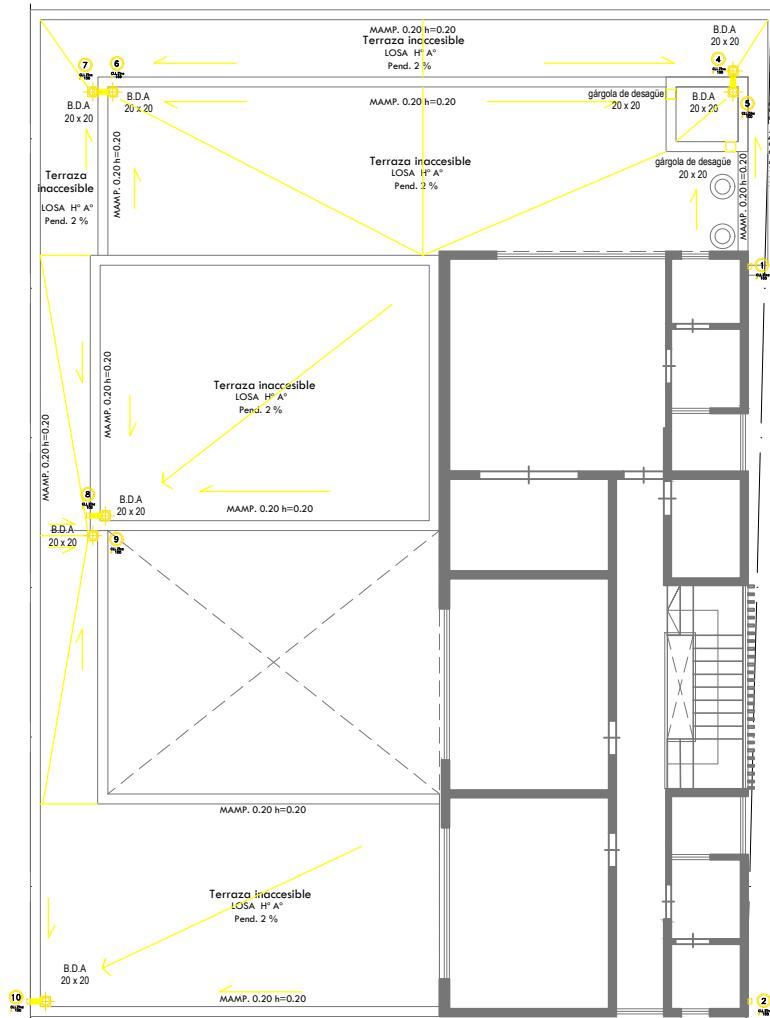



PLANTA ALTA

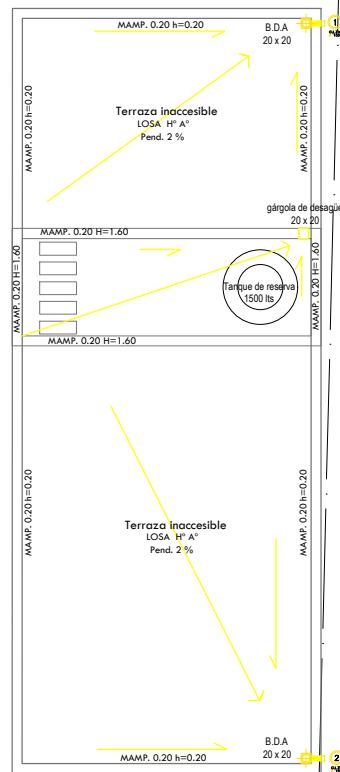


PLANTA DE TECHOS

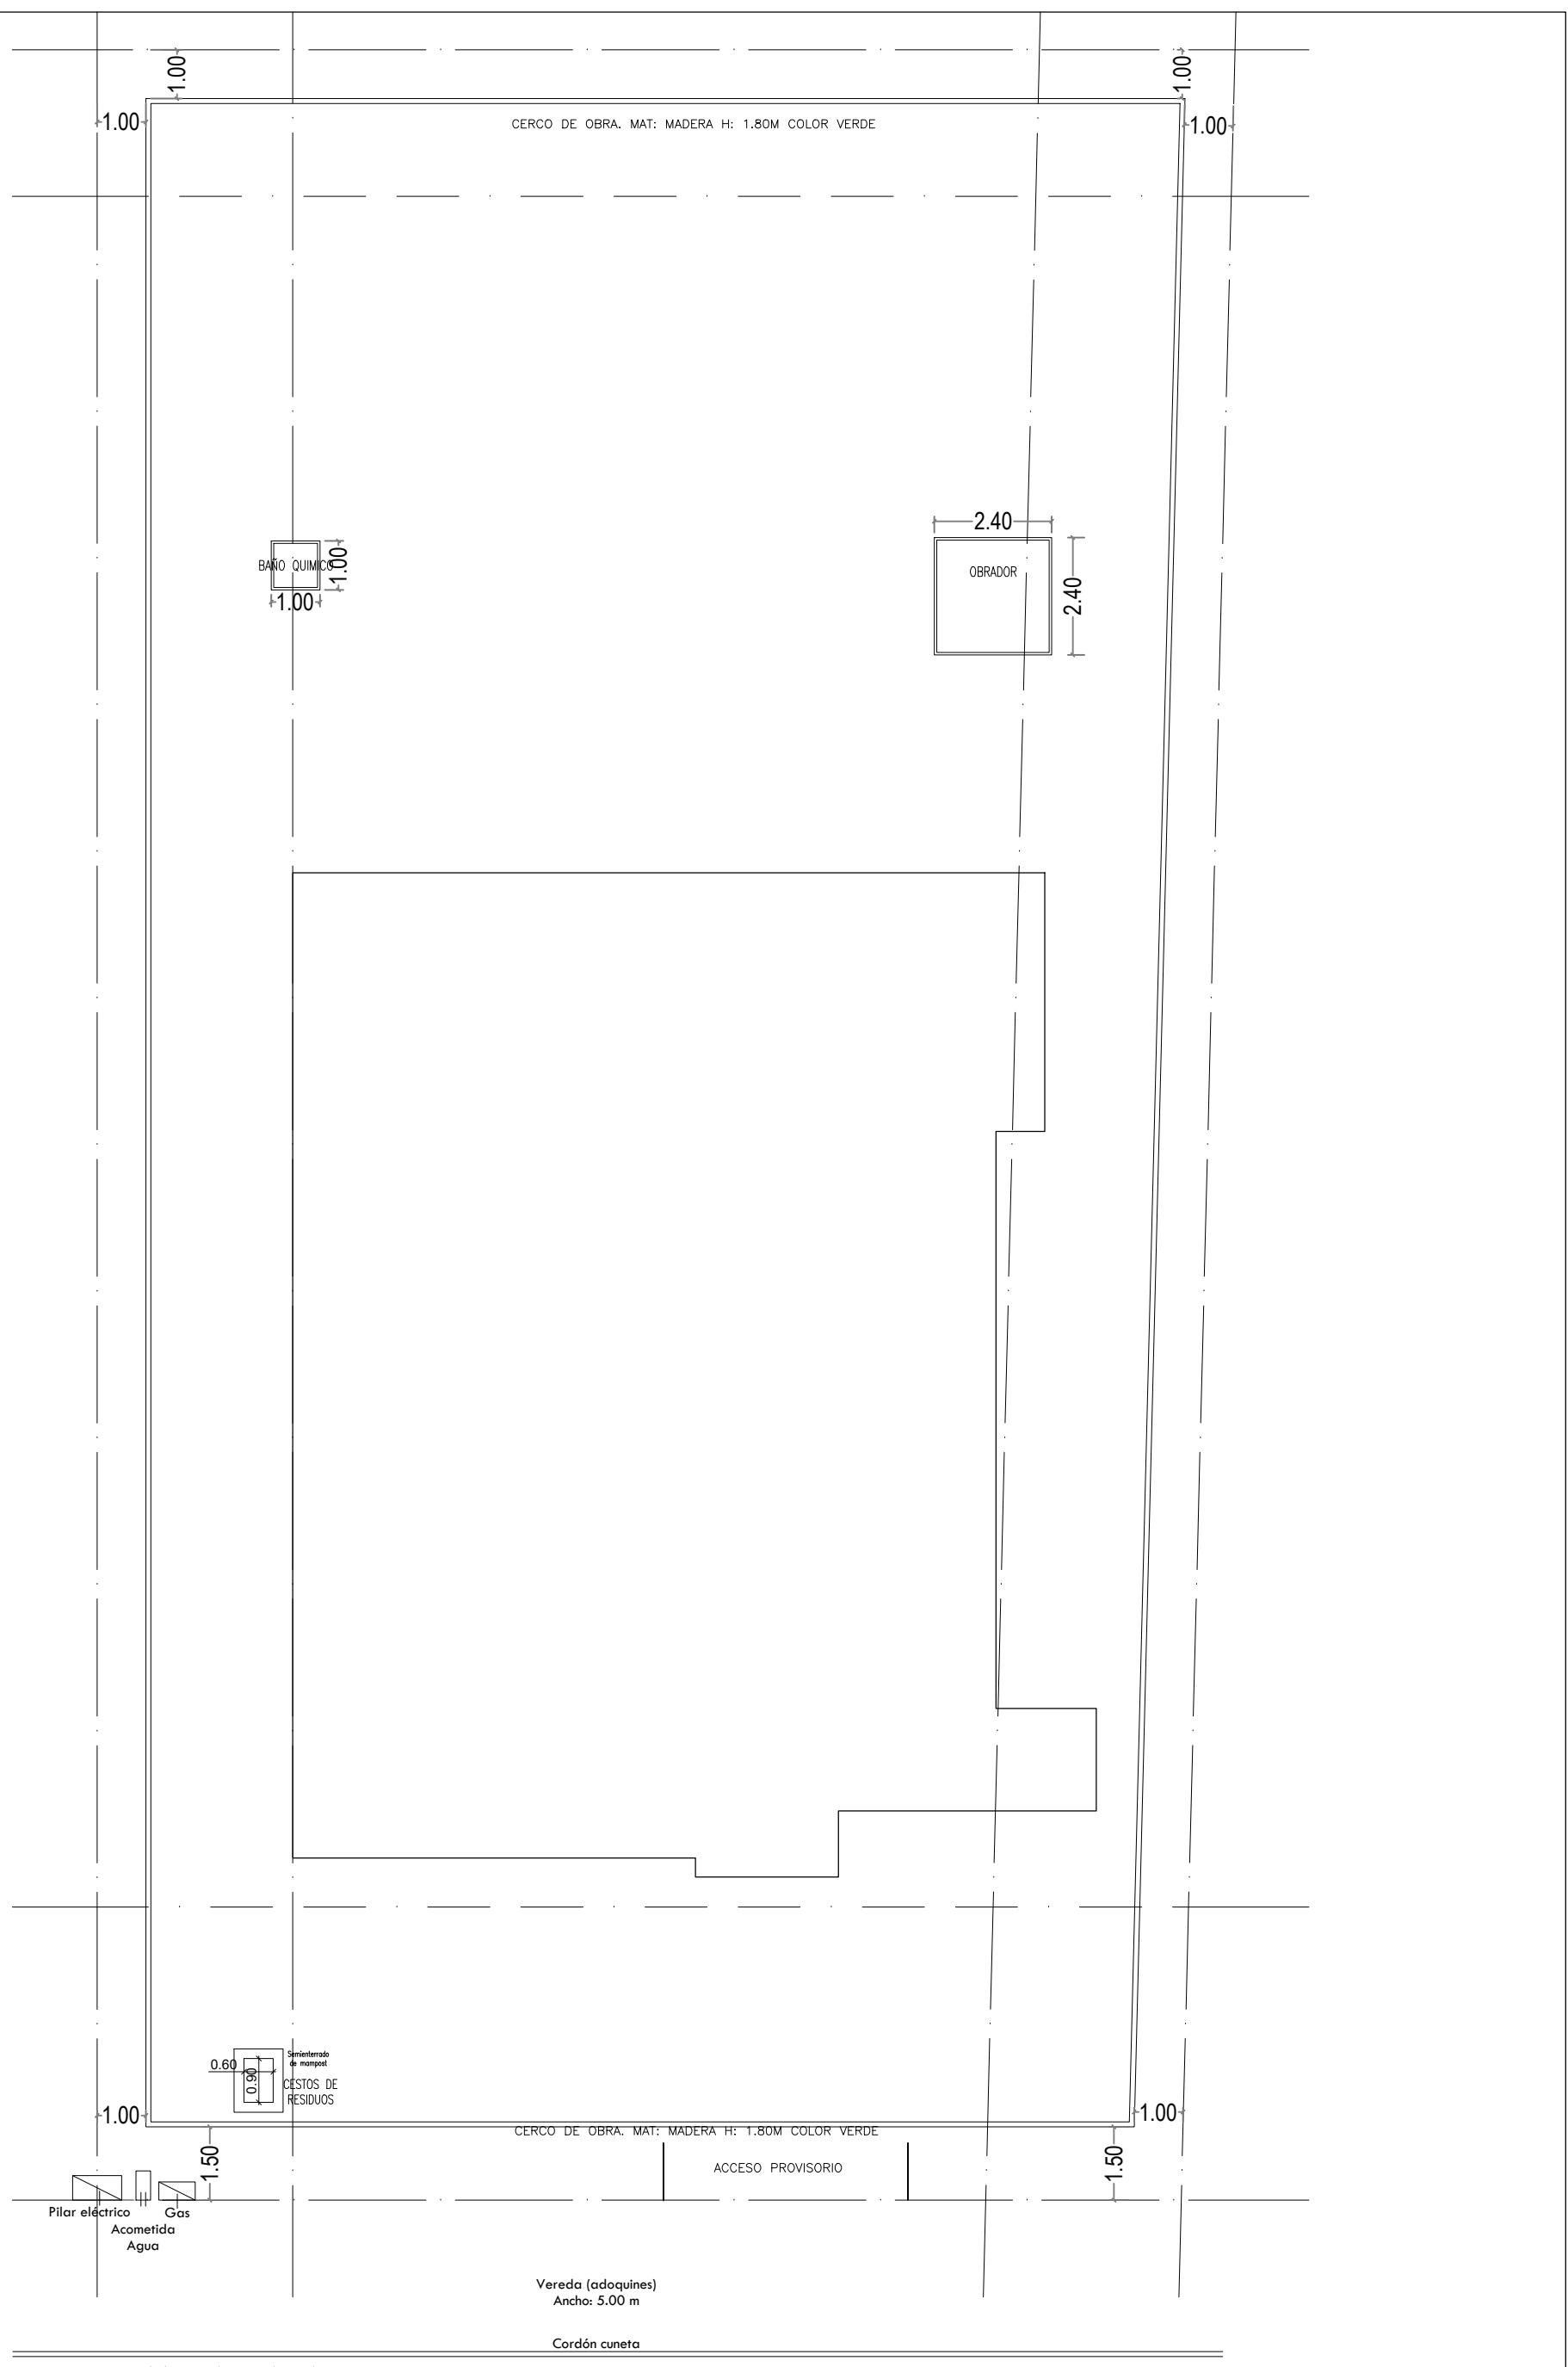


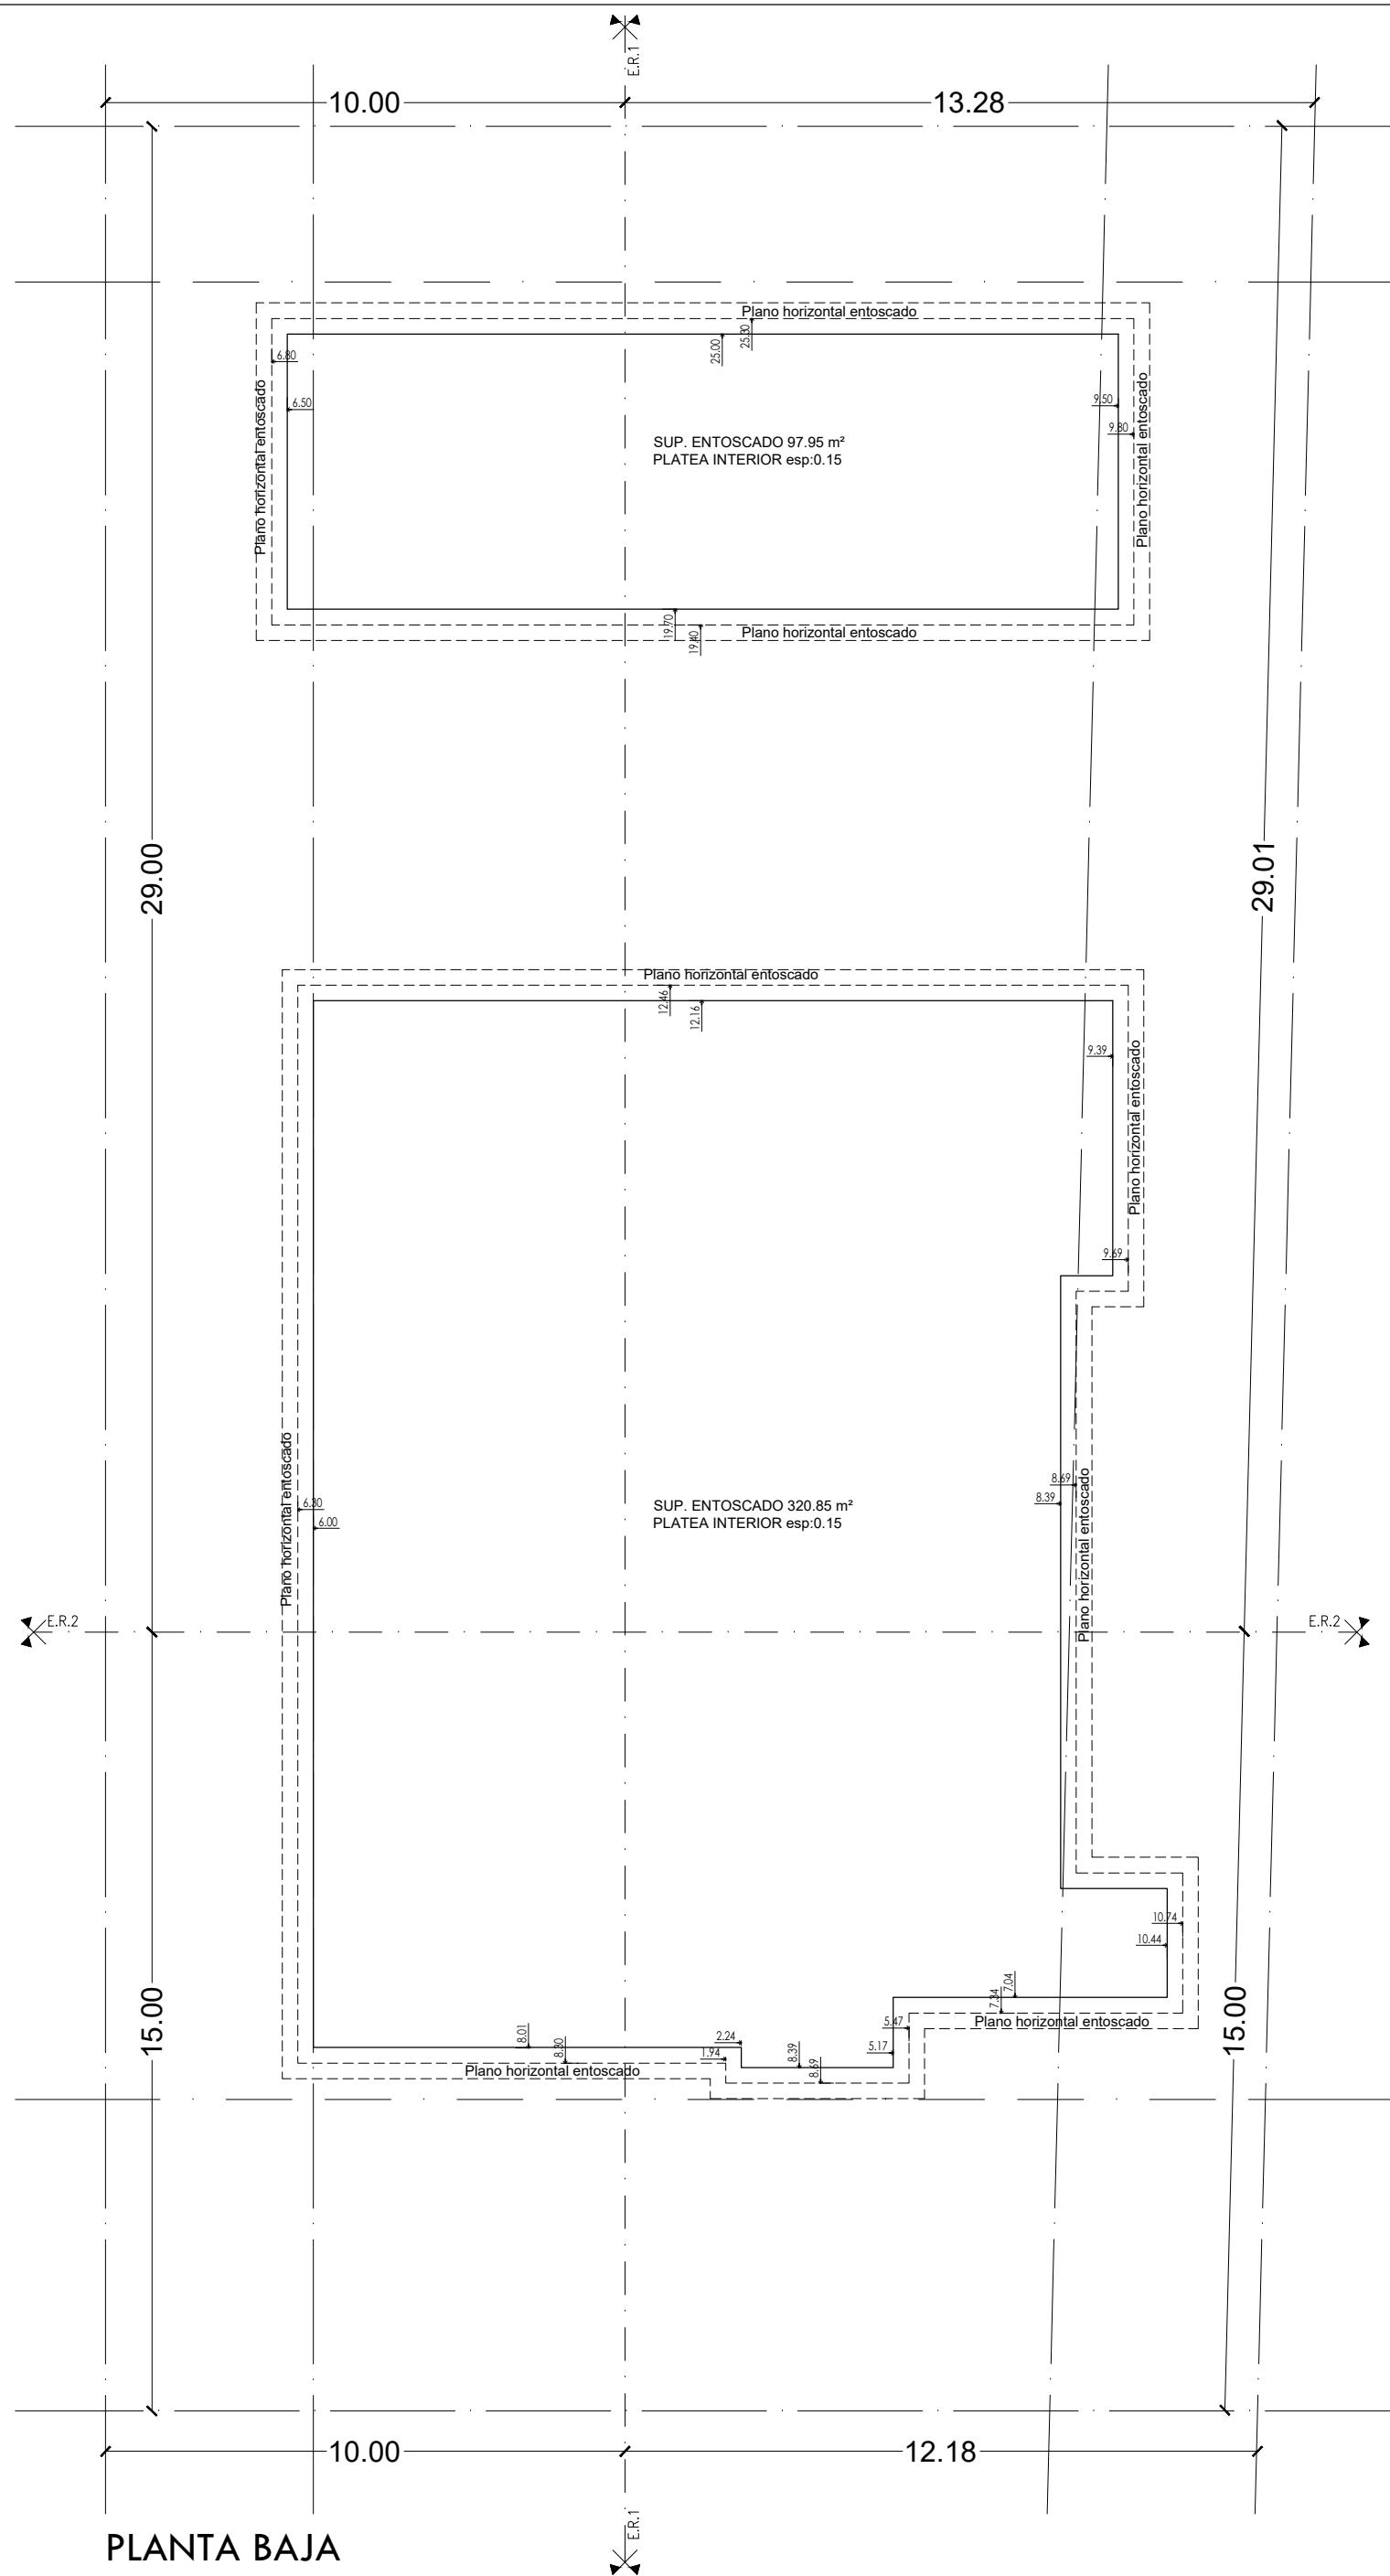

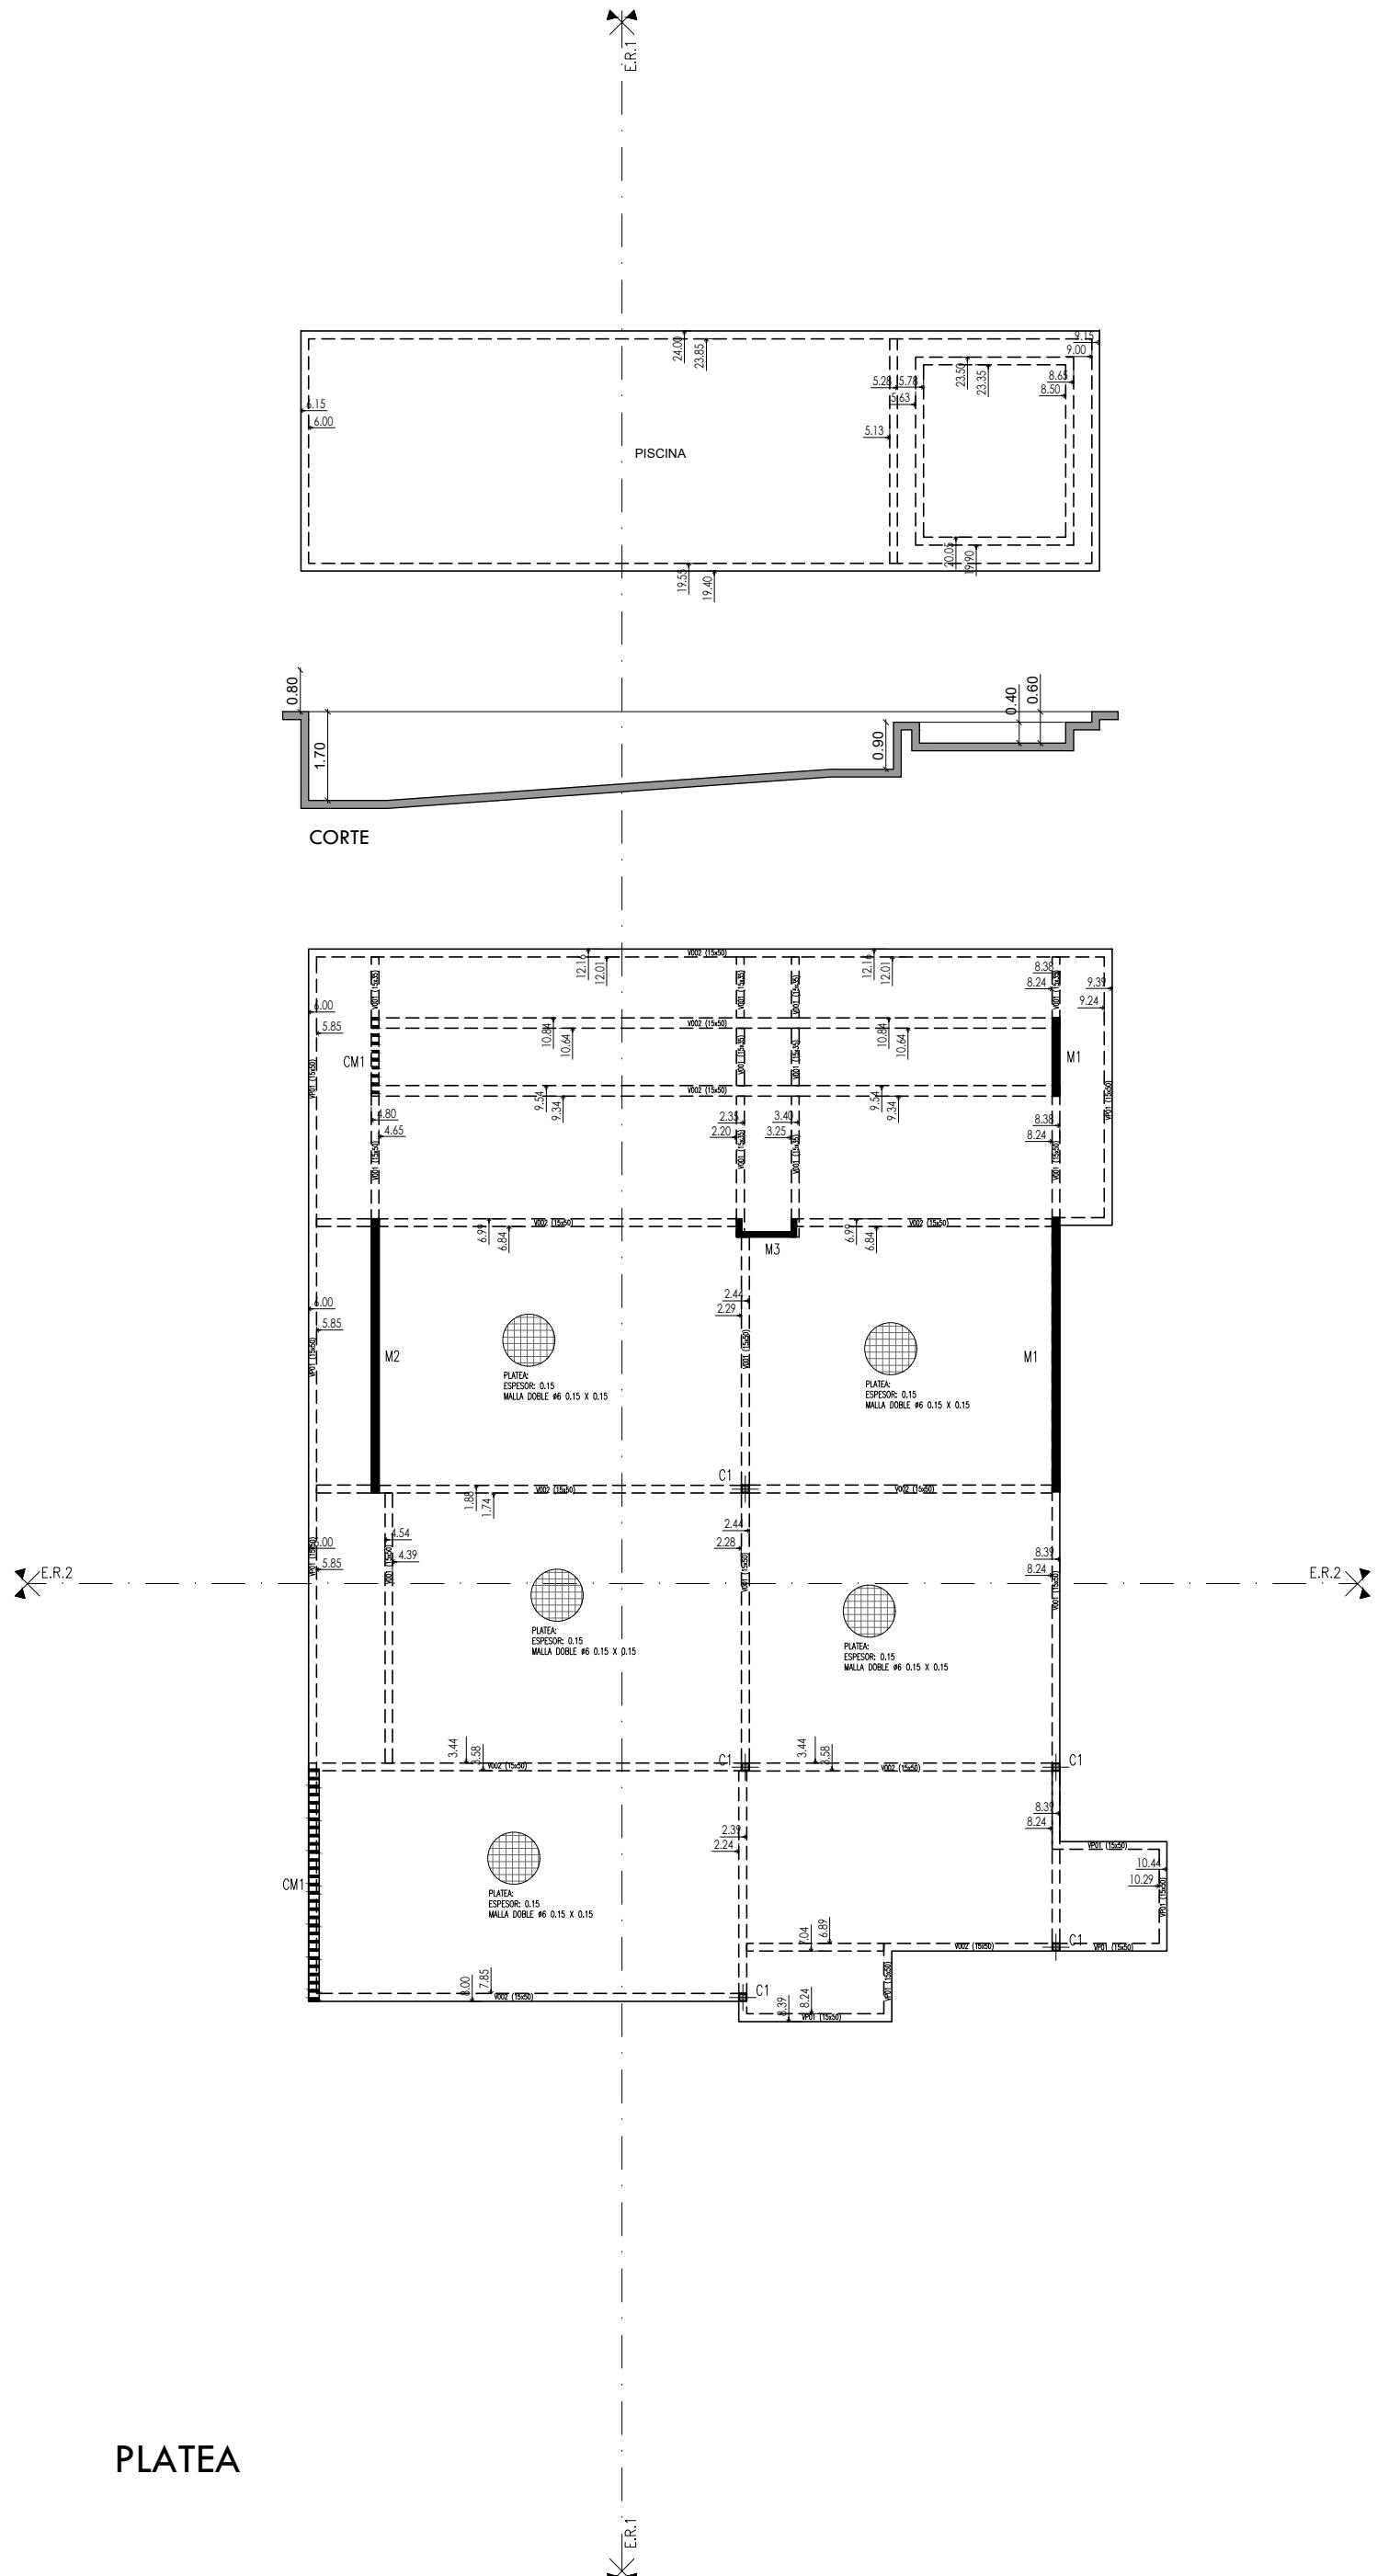


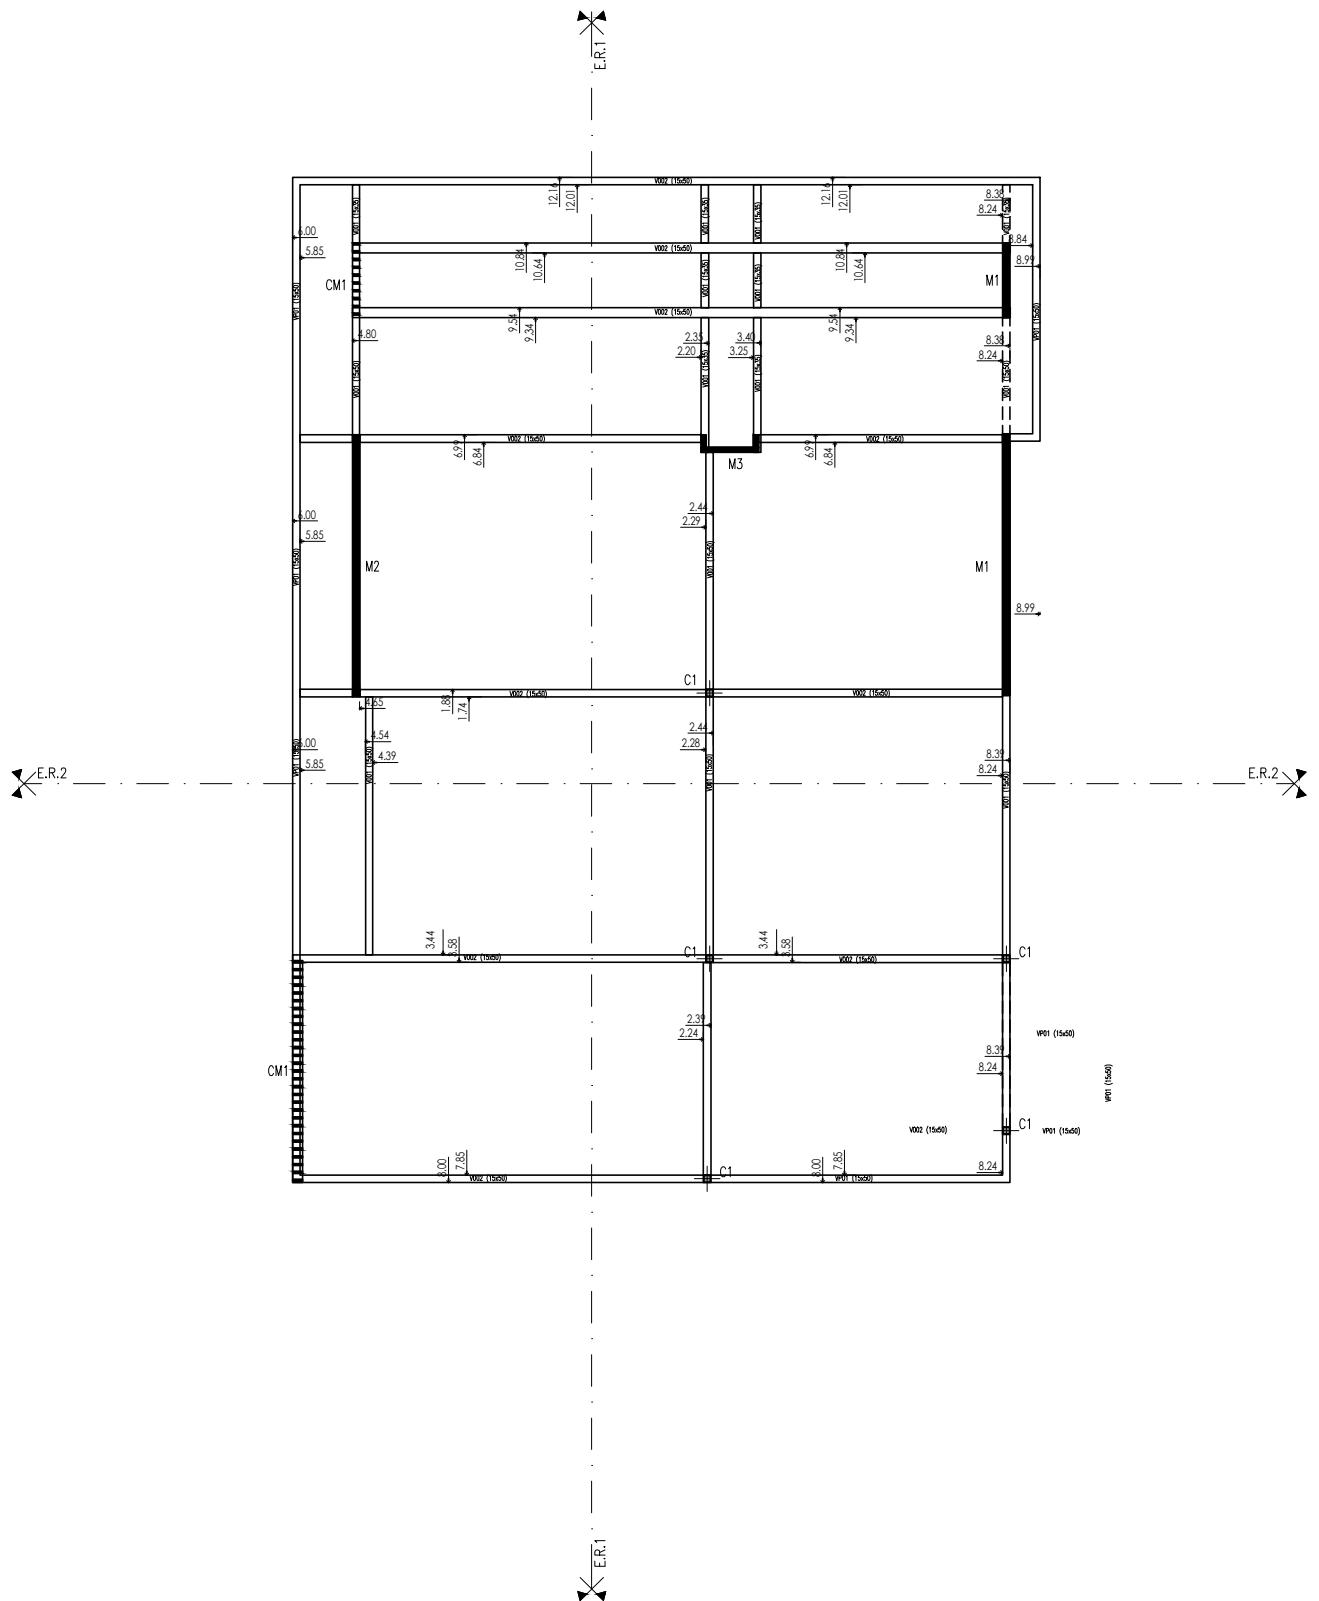




ESTRUCTURA S/PLANTA BAJA

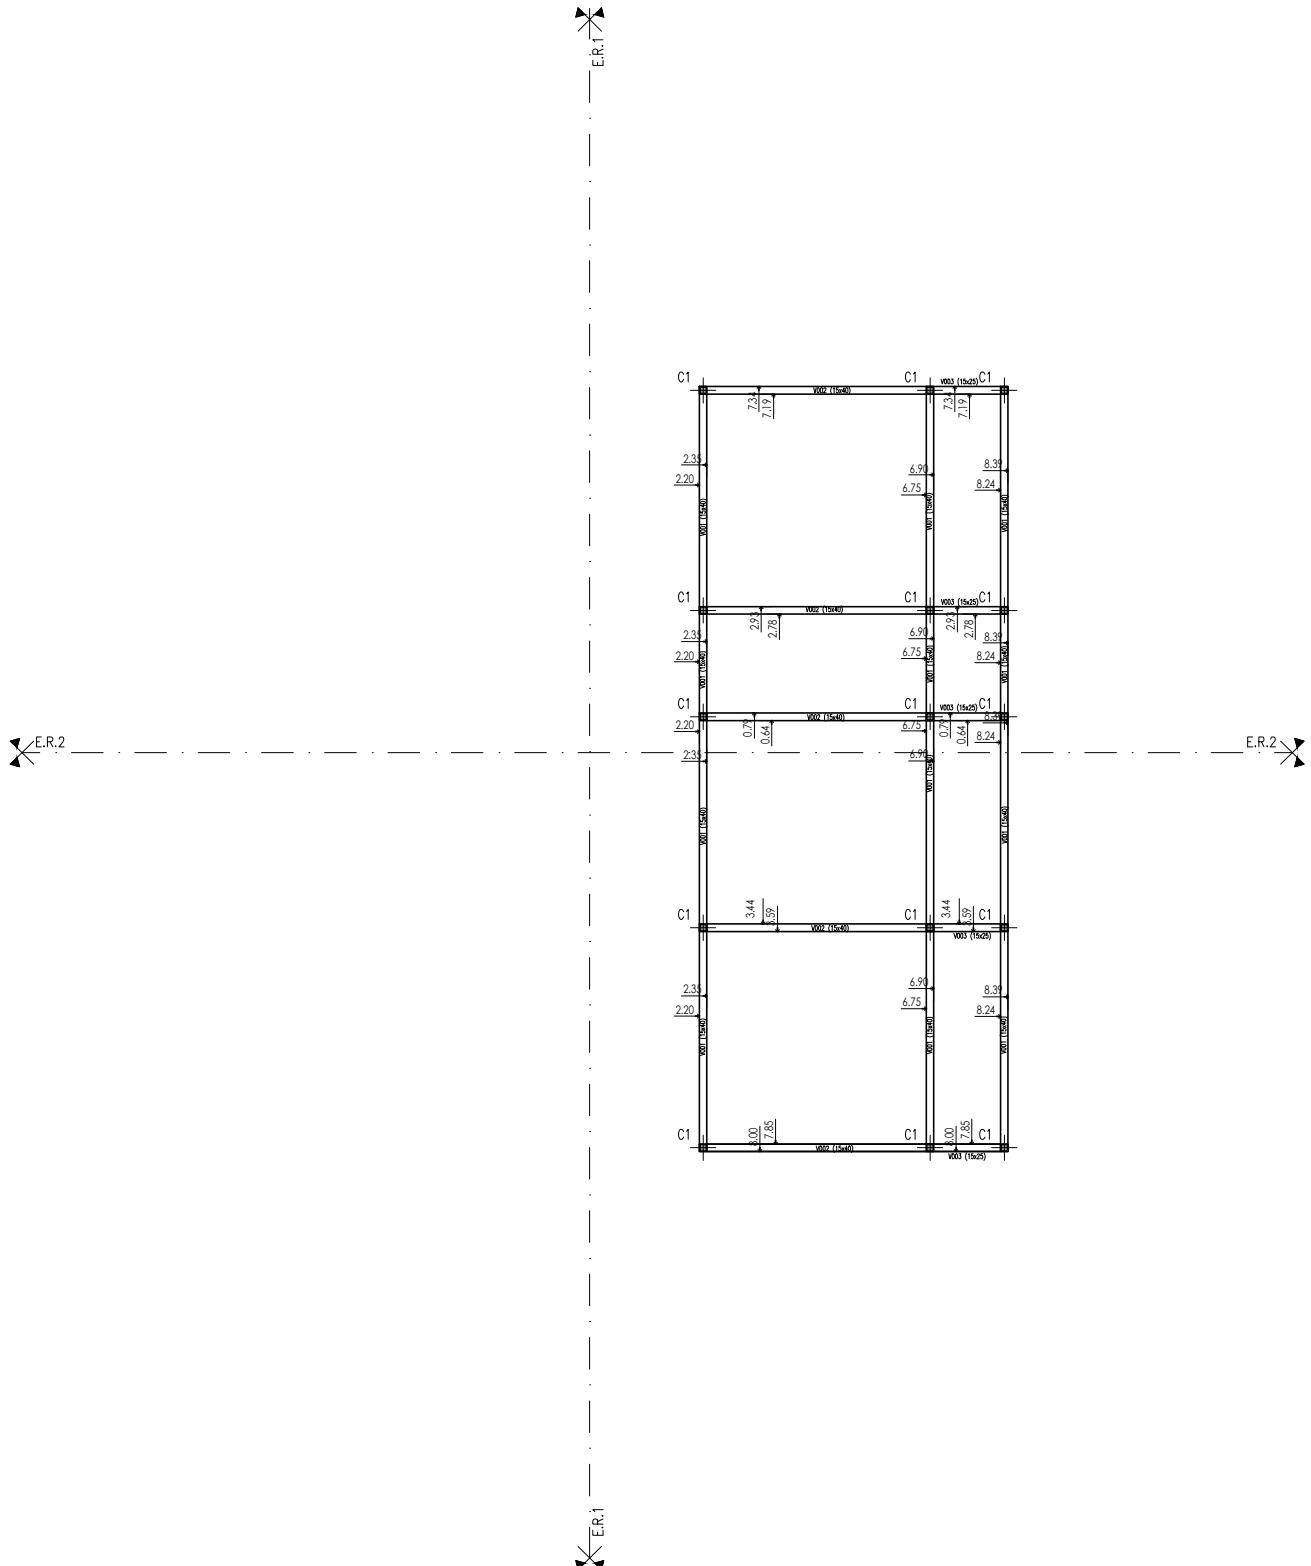

ESTRUCTURA S/PLANTA ALTA

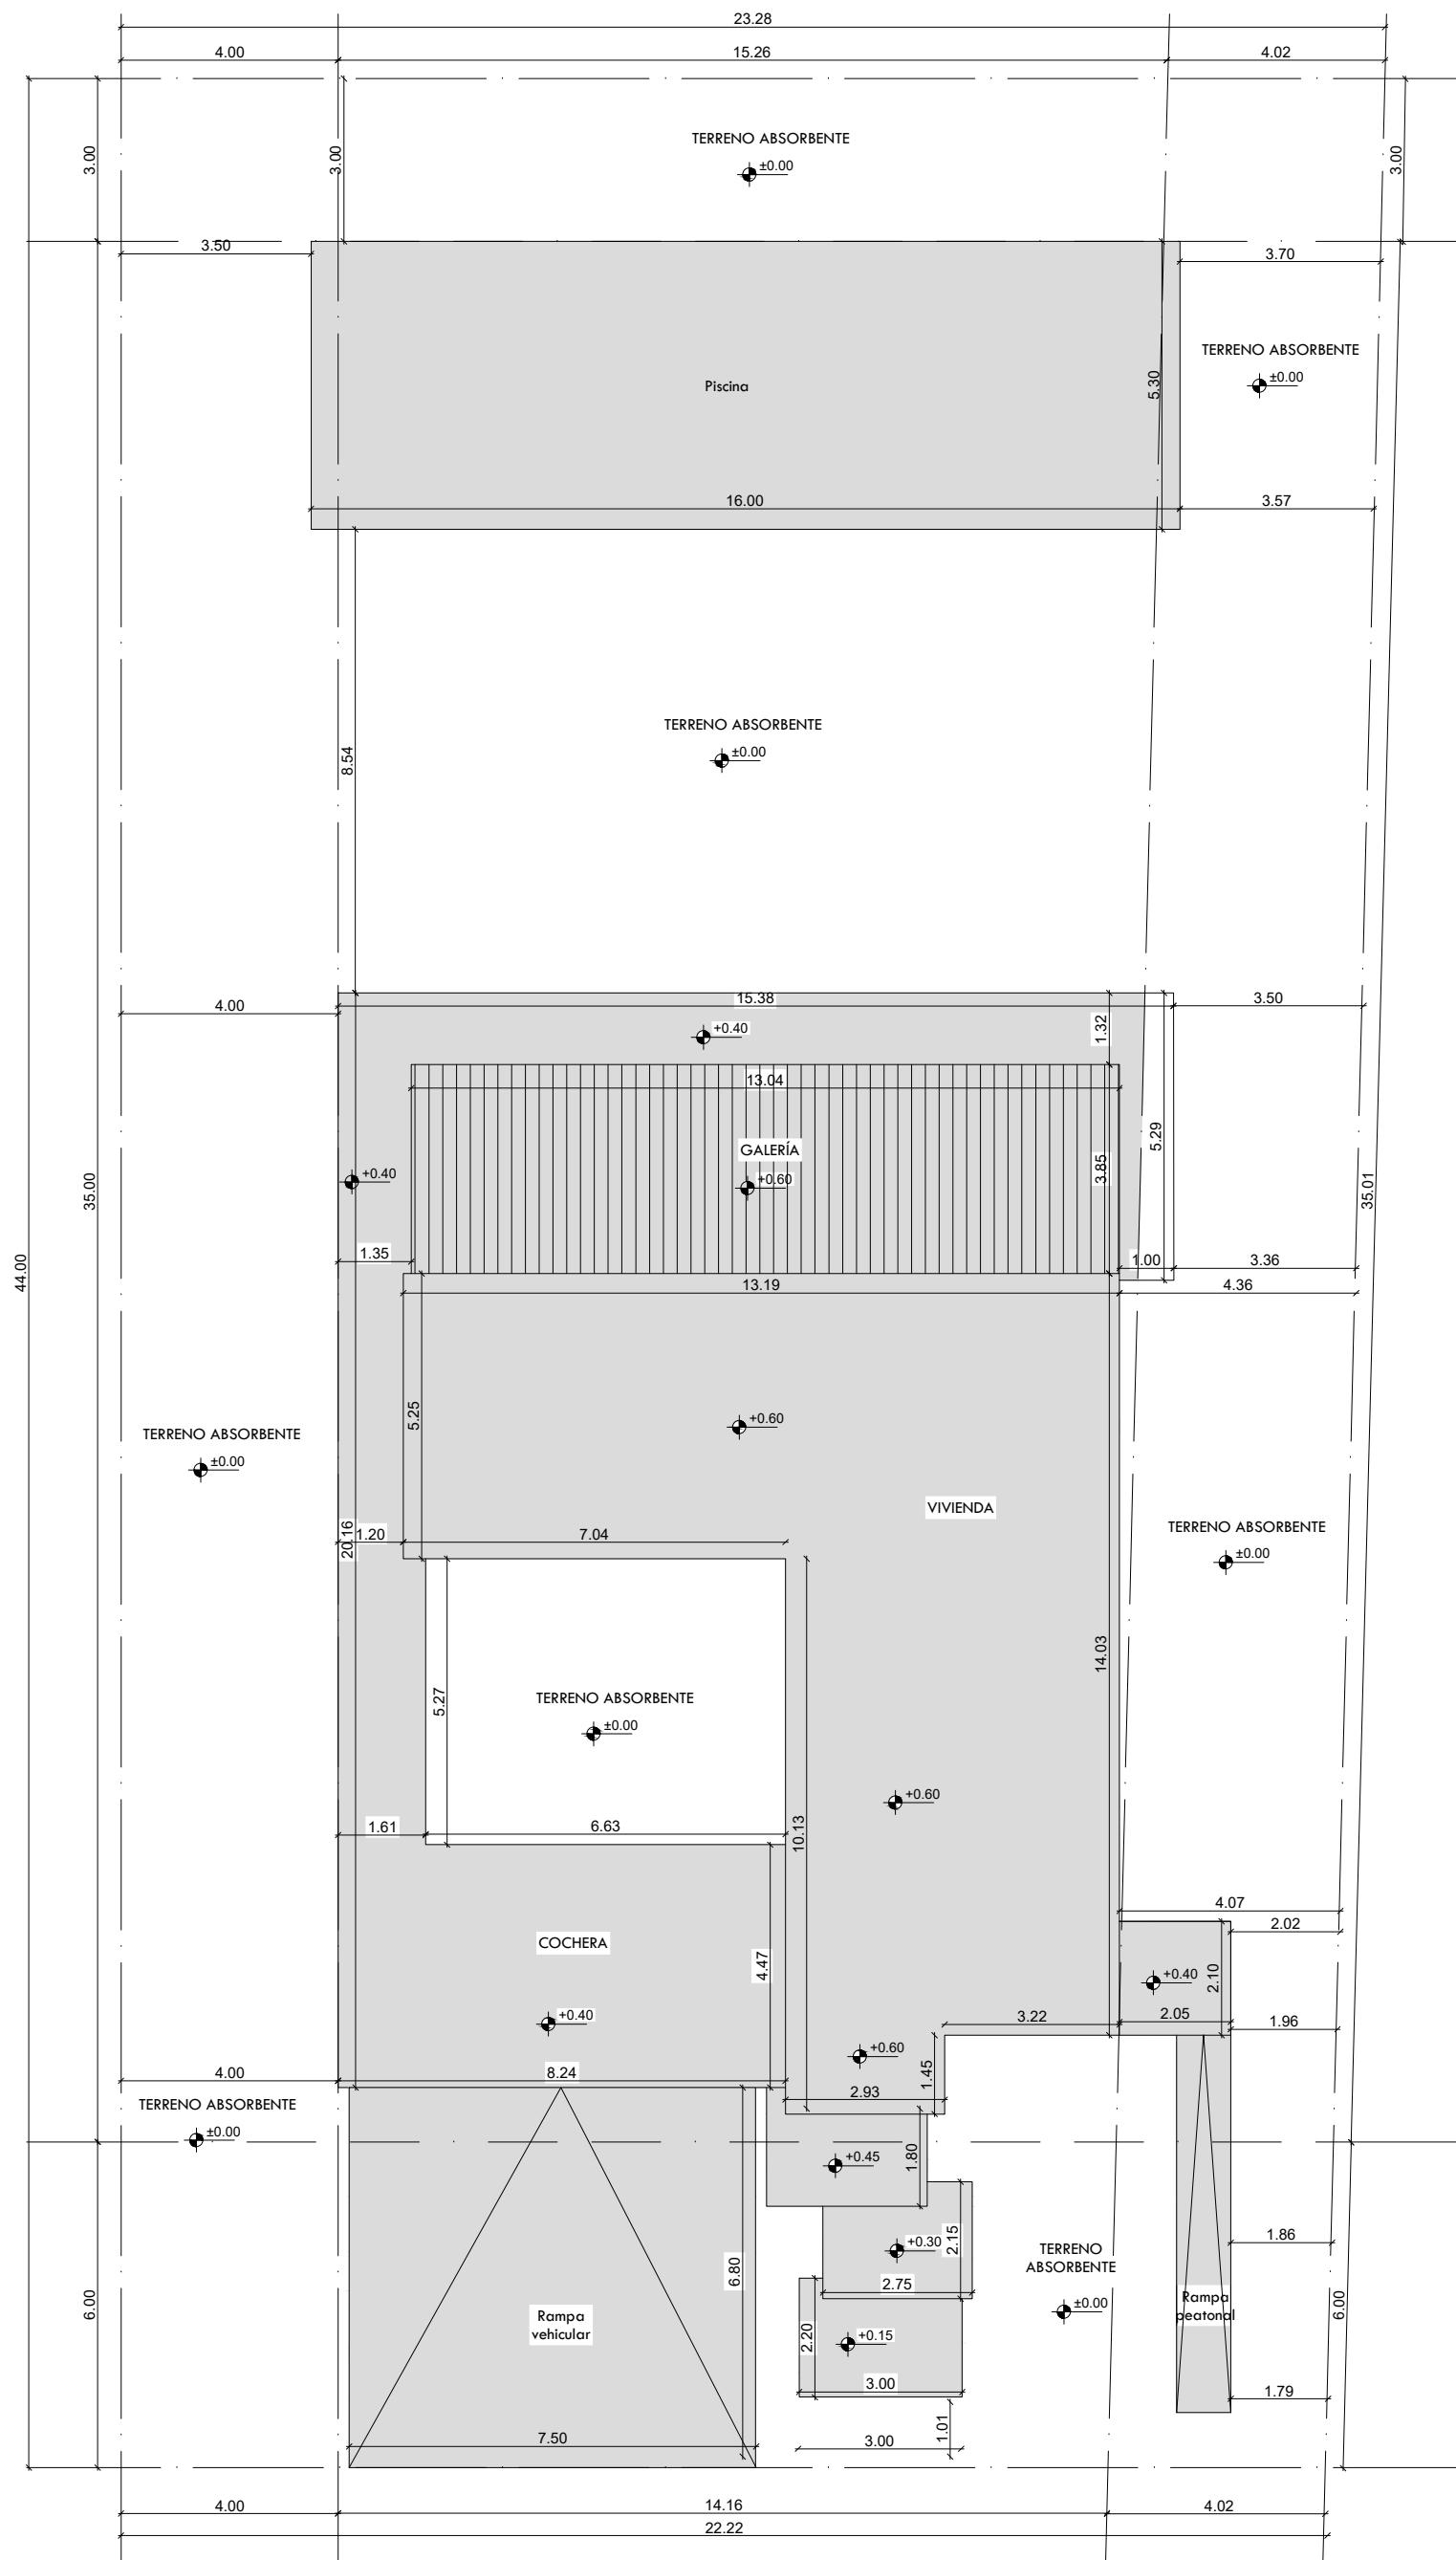


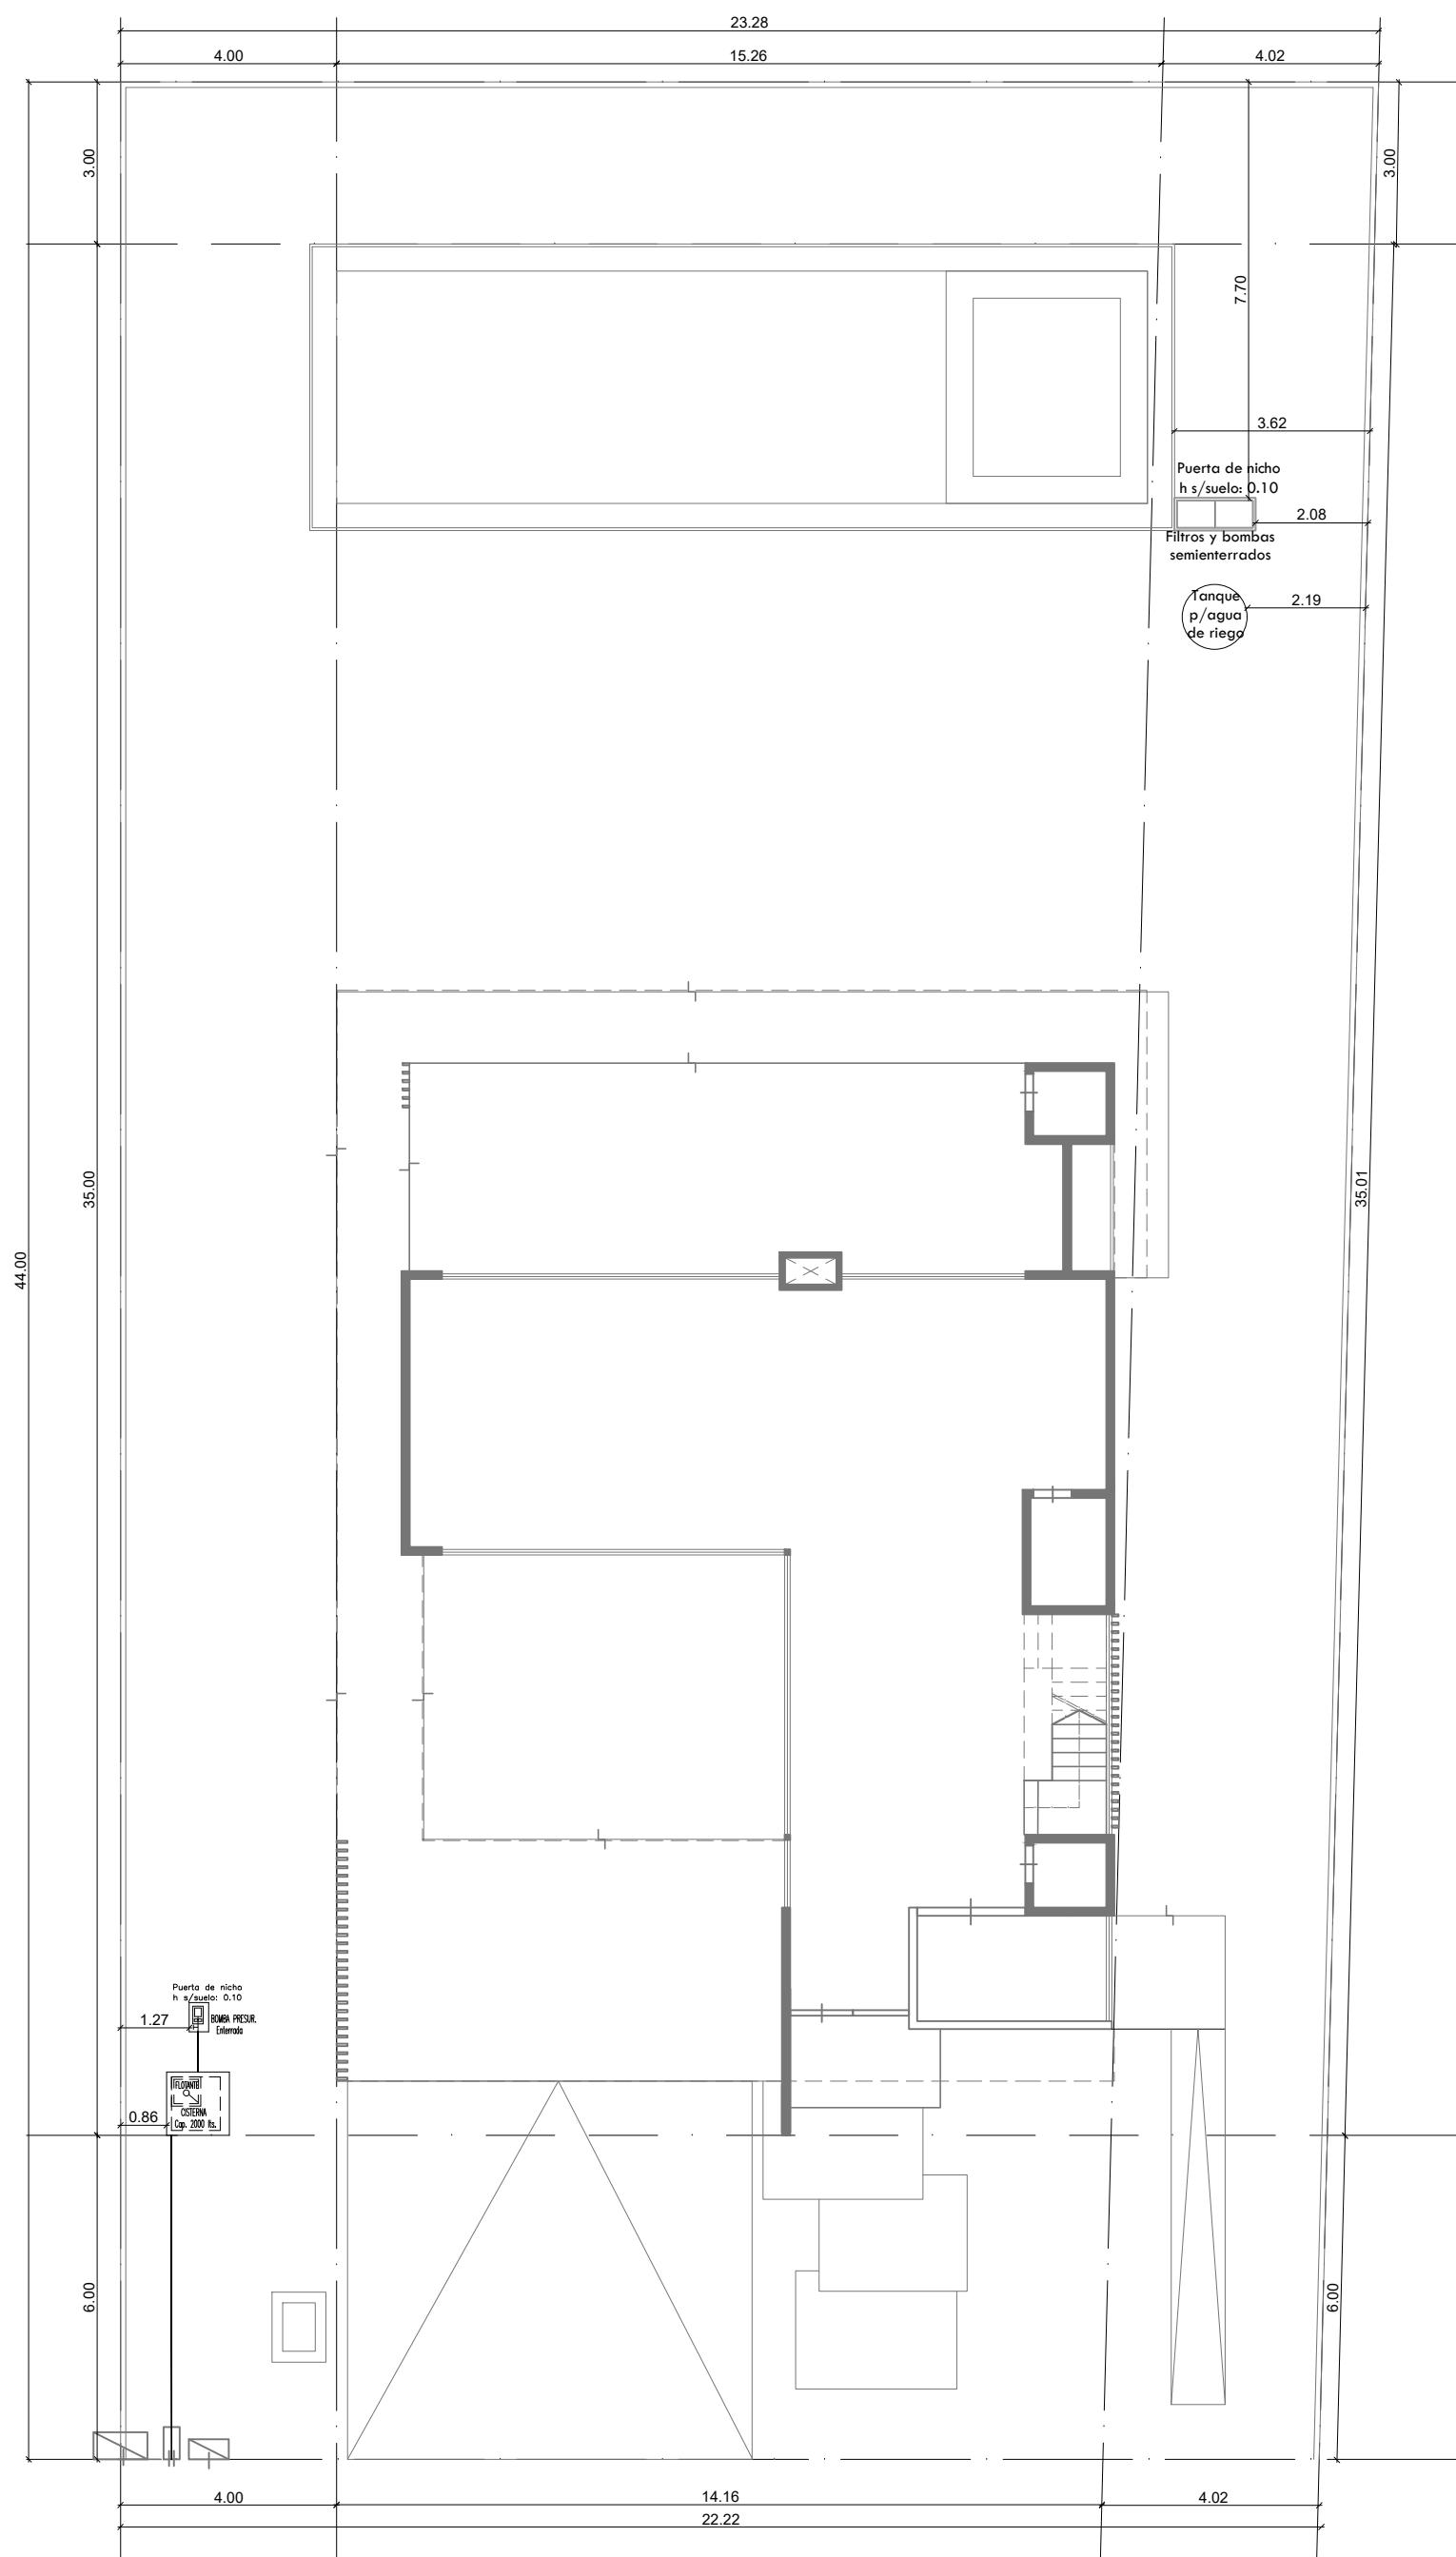


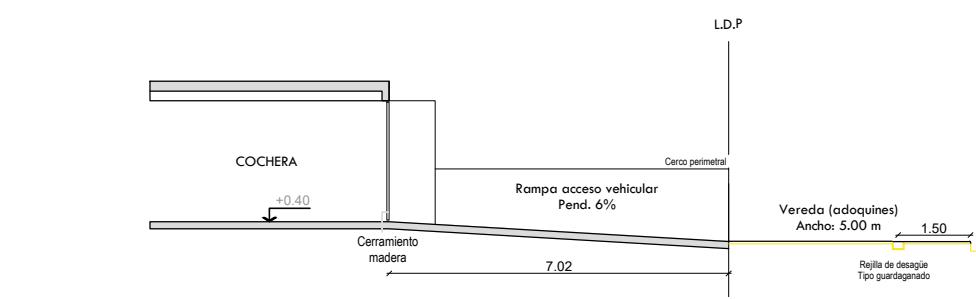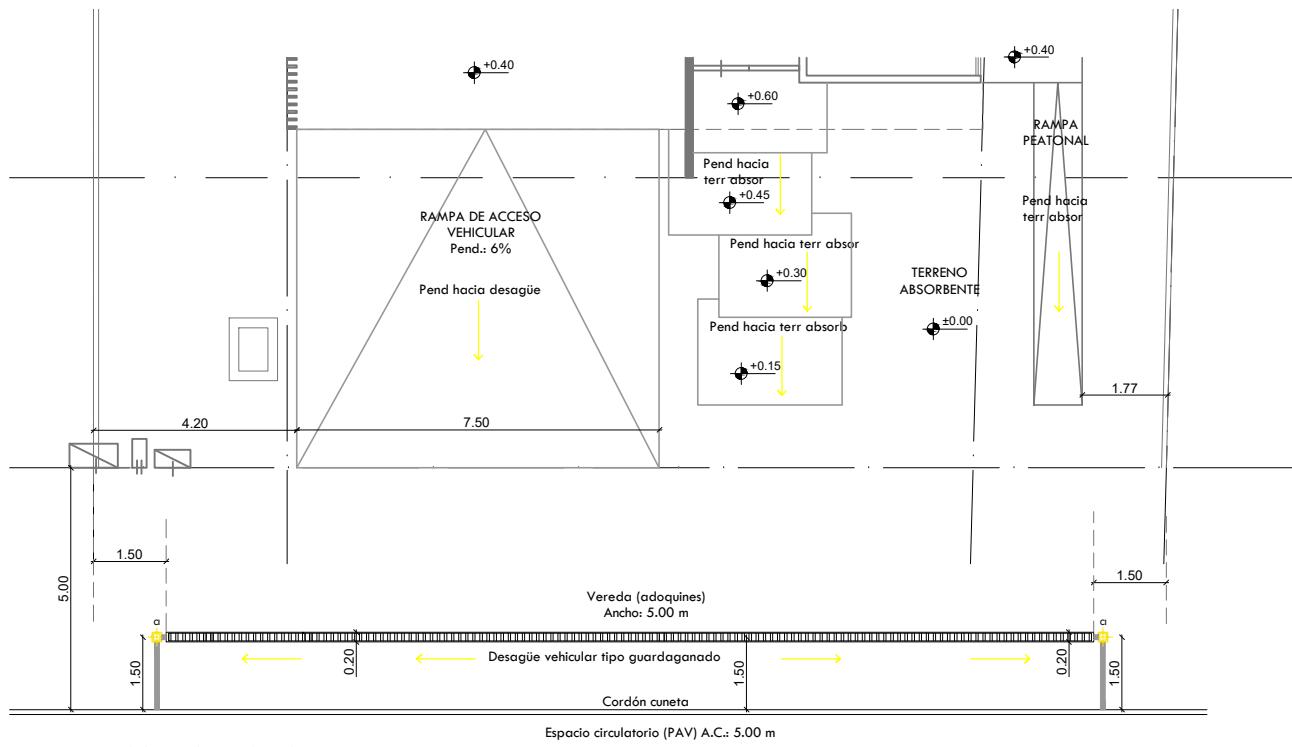

CORTE


DETALLE SILUETA DEL TERRENO


Esc.: 1:100

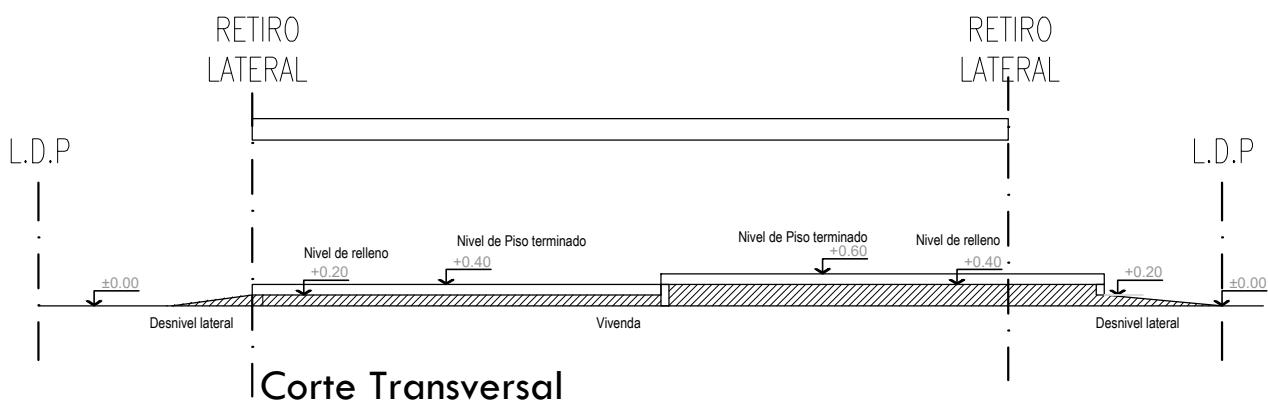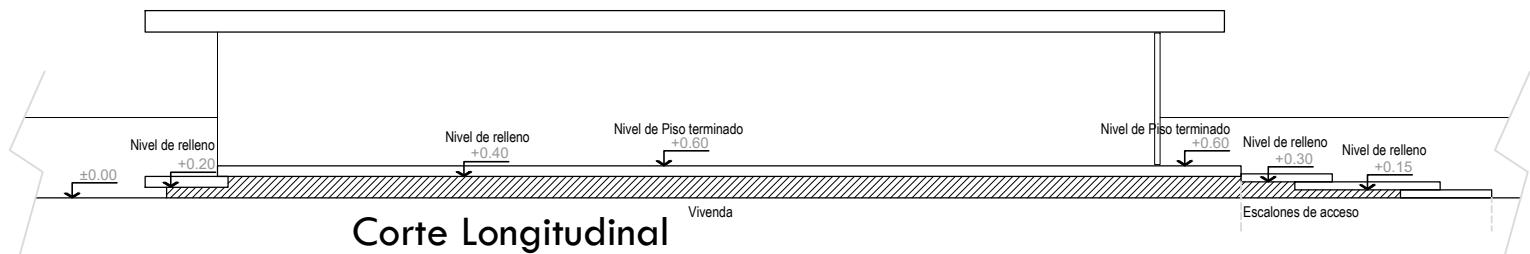


DETALLE ENCUENTRO CERCO FONTAL-NIVEL DE RELLENO


Esc.: 1:100

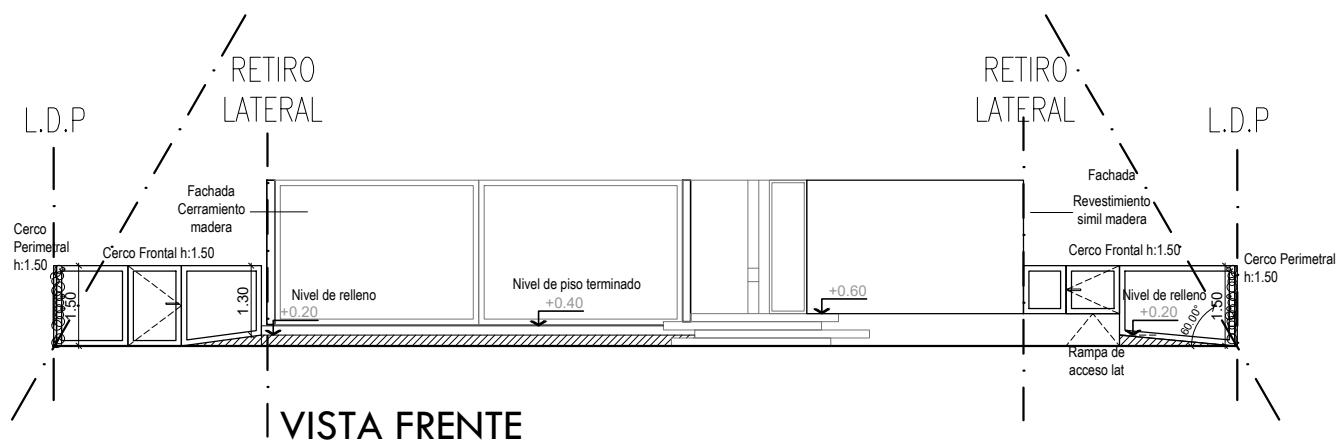


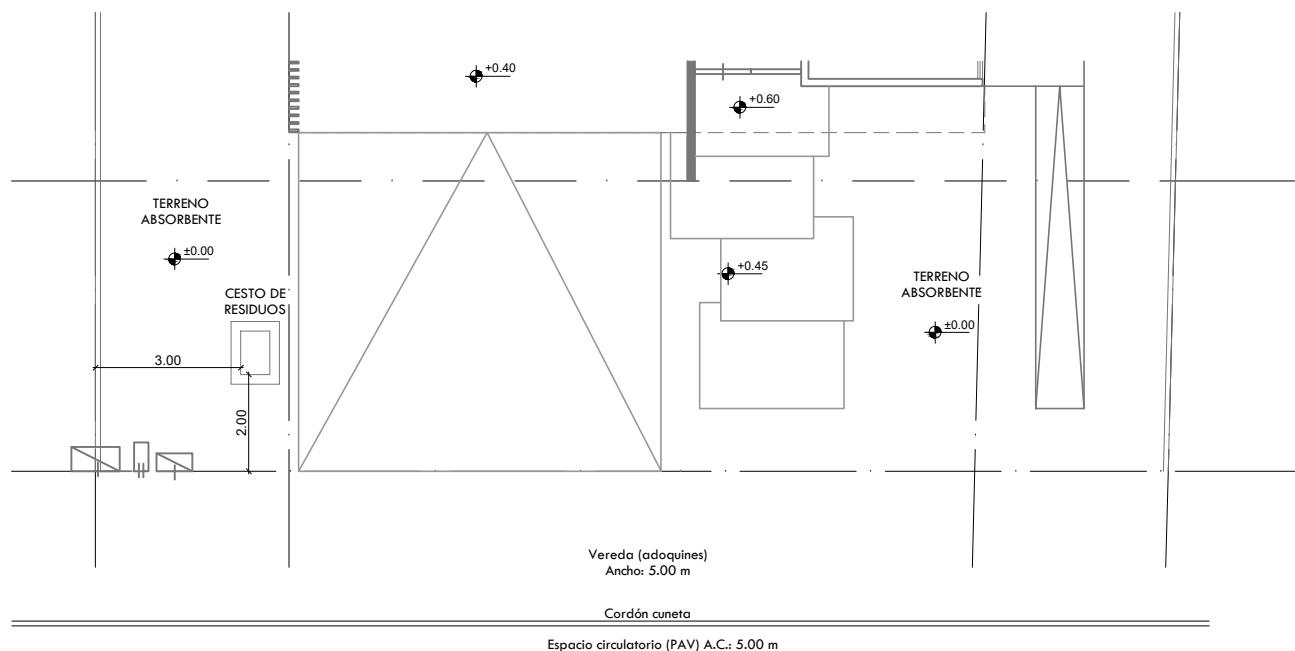

PLANTA BAJA

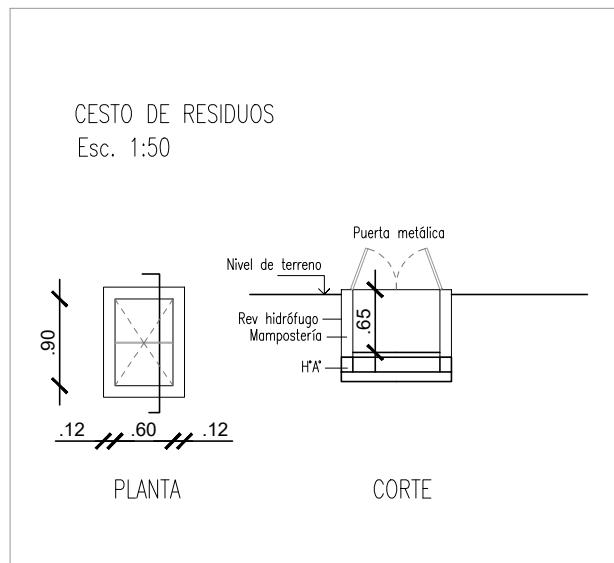

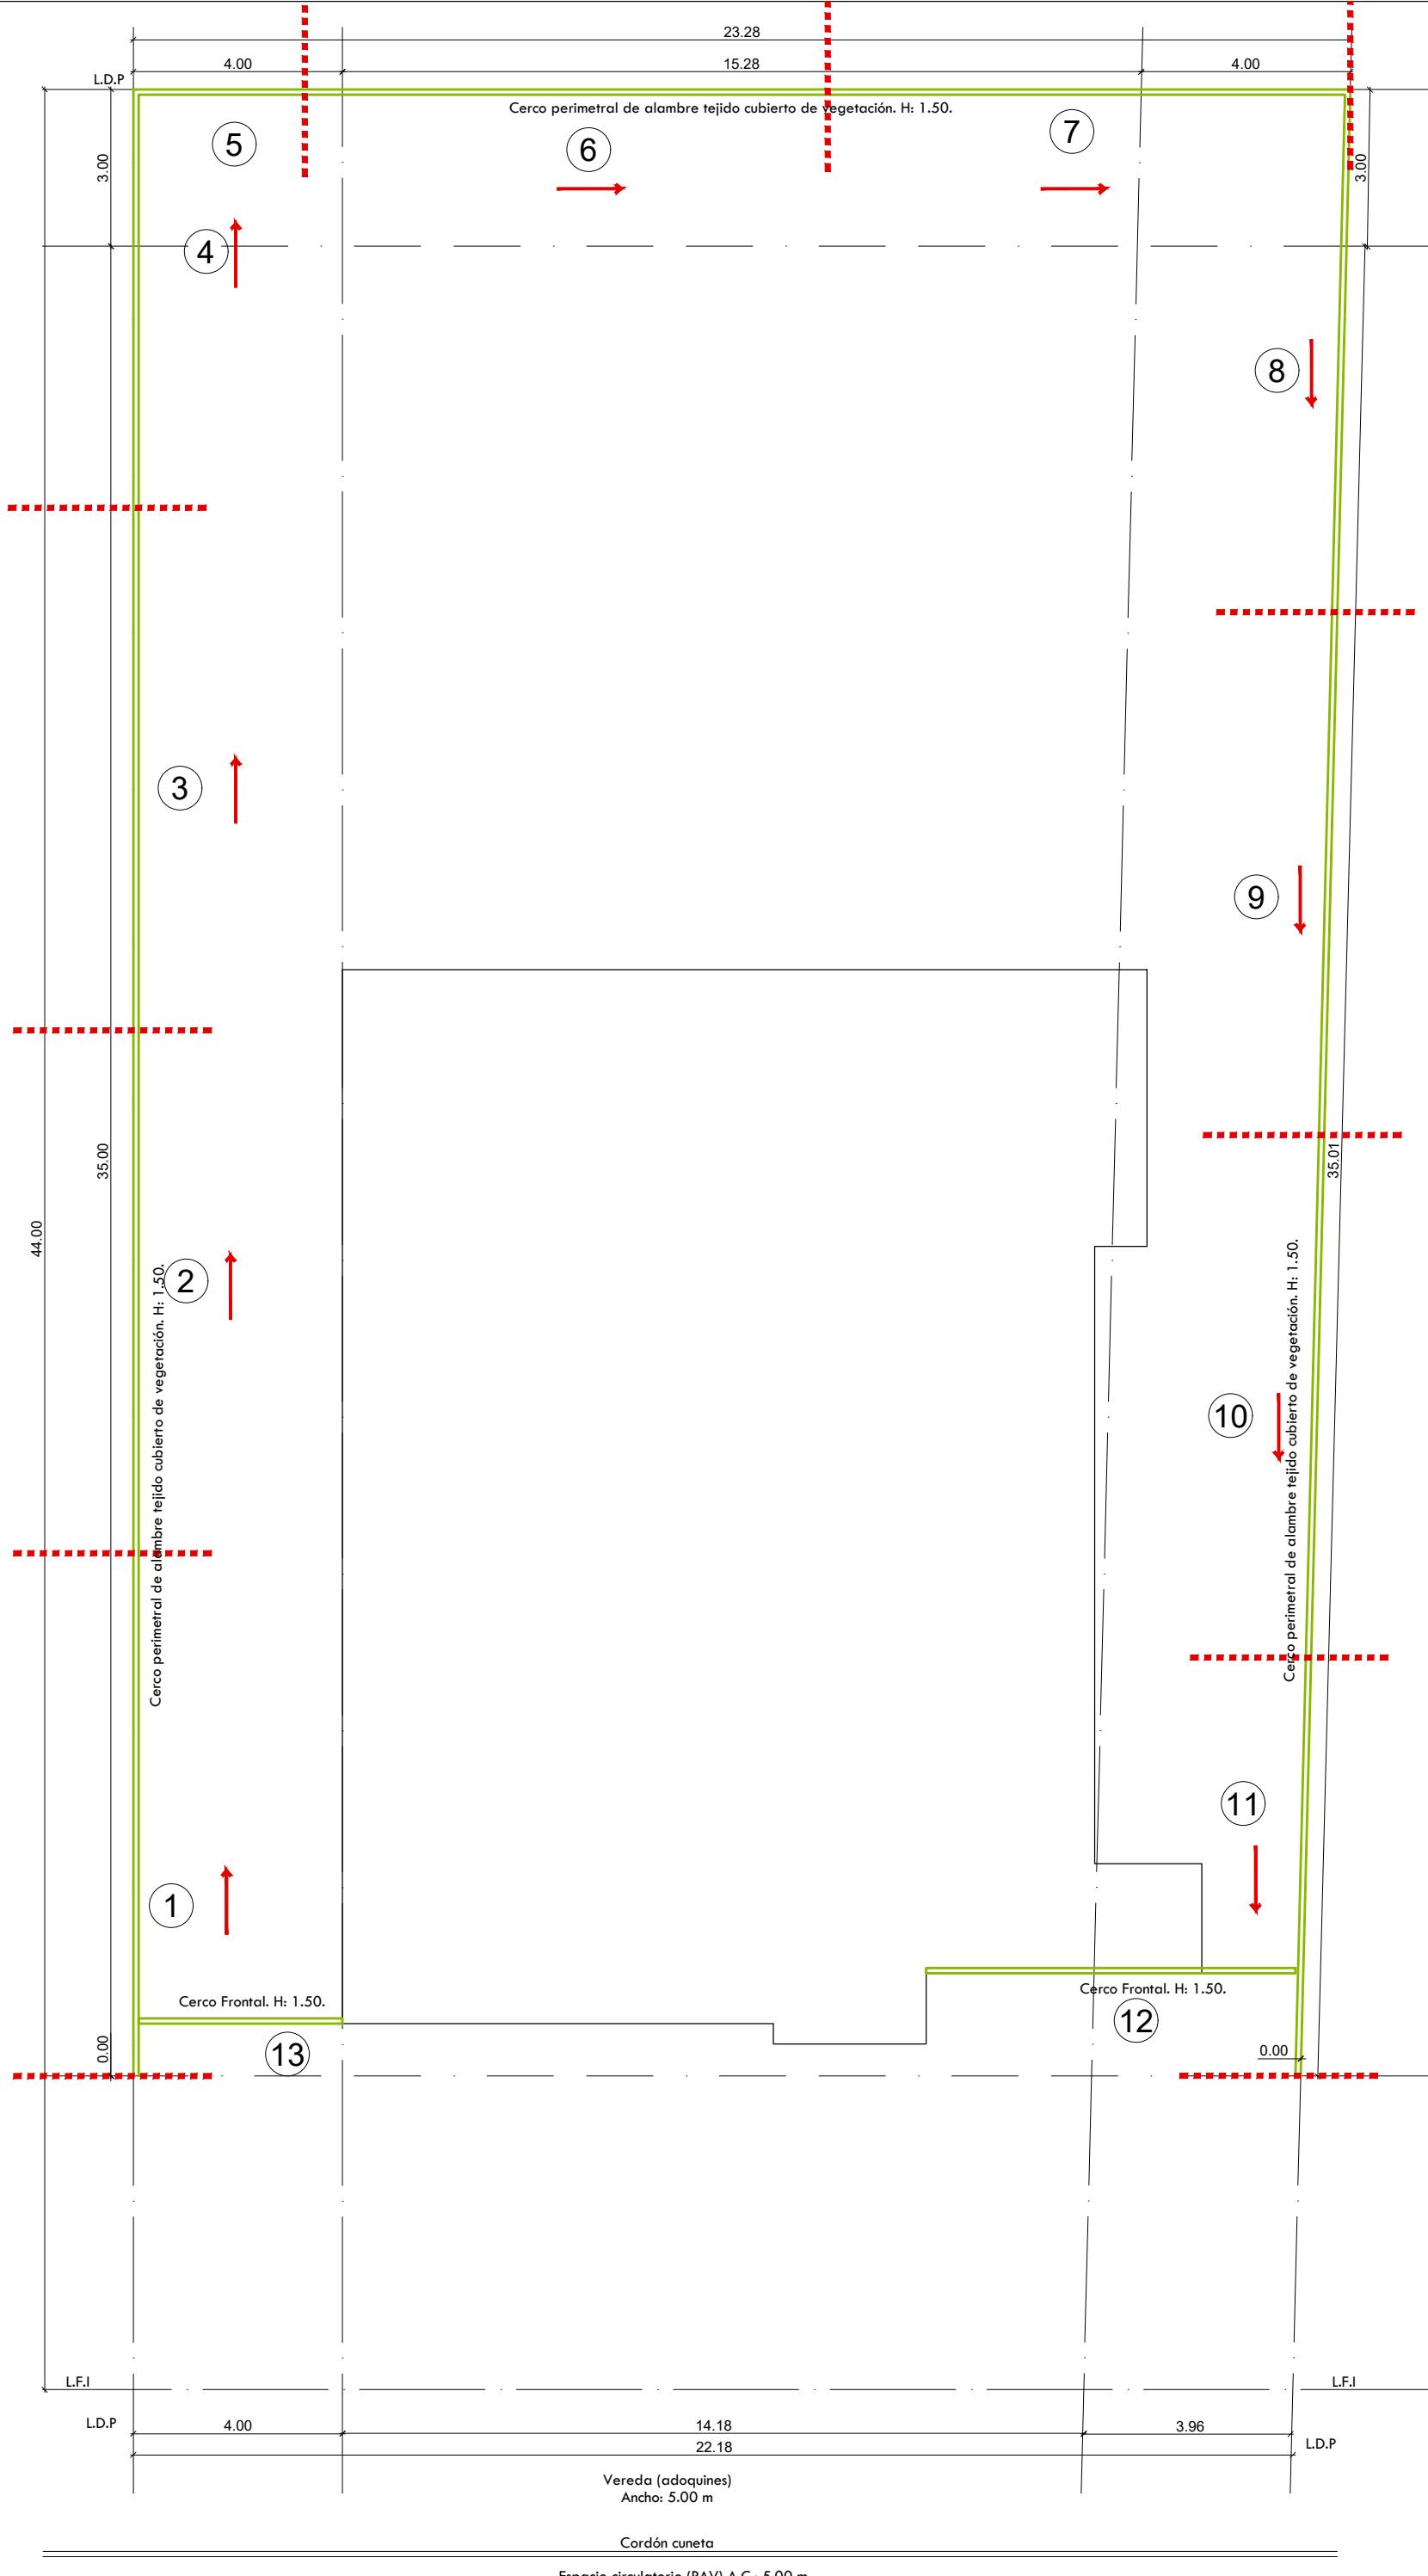

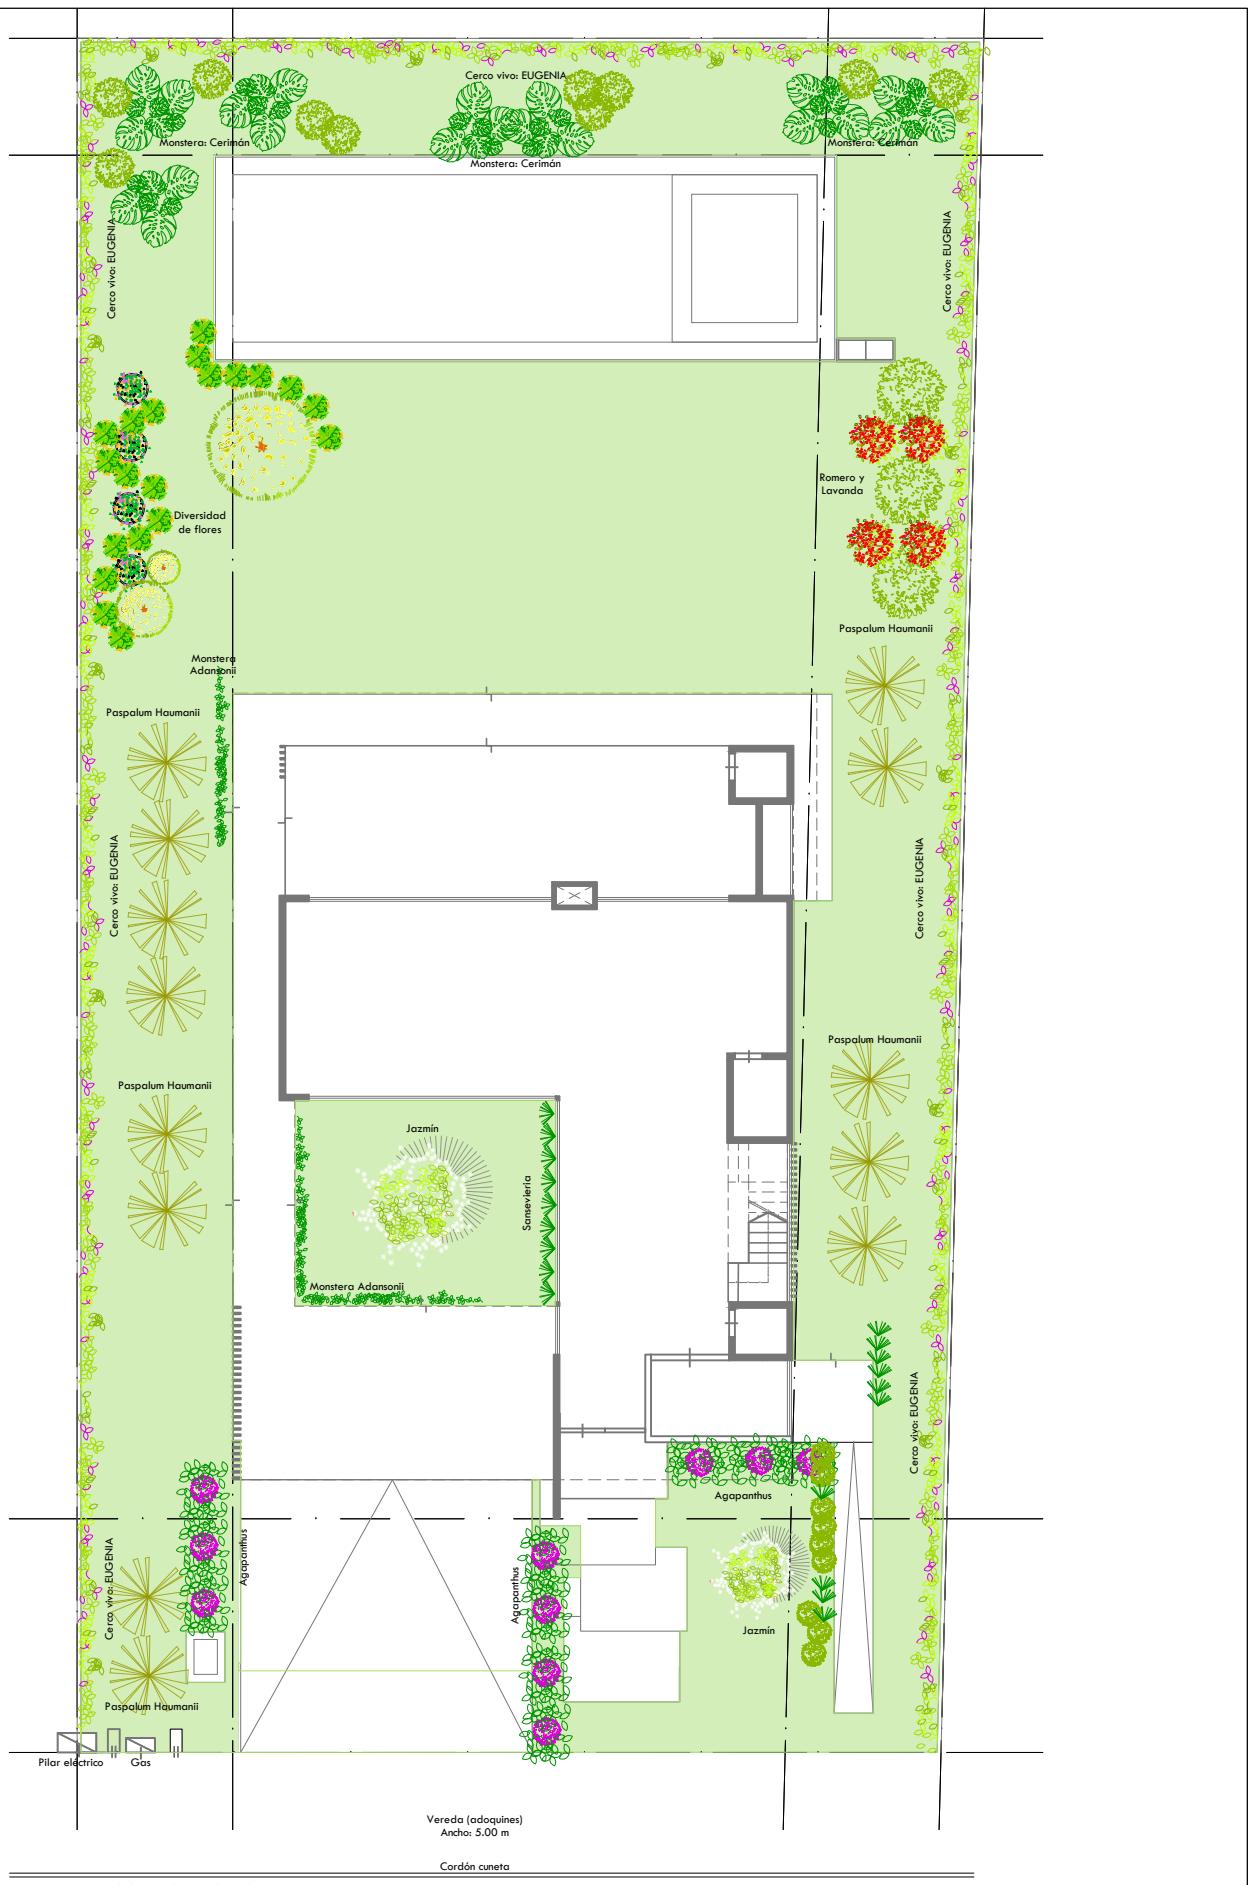

PLANTA BAJA

Cordón cuneta

Espacio circulatorio (PAV) A.C.: 5.00 m

**El terreno no cuenta con
vegetación existente**

